

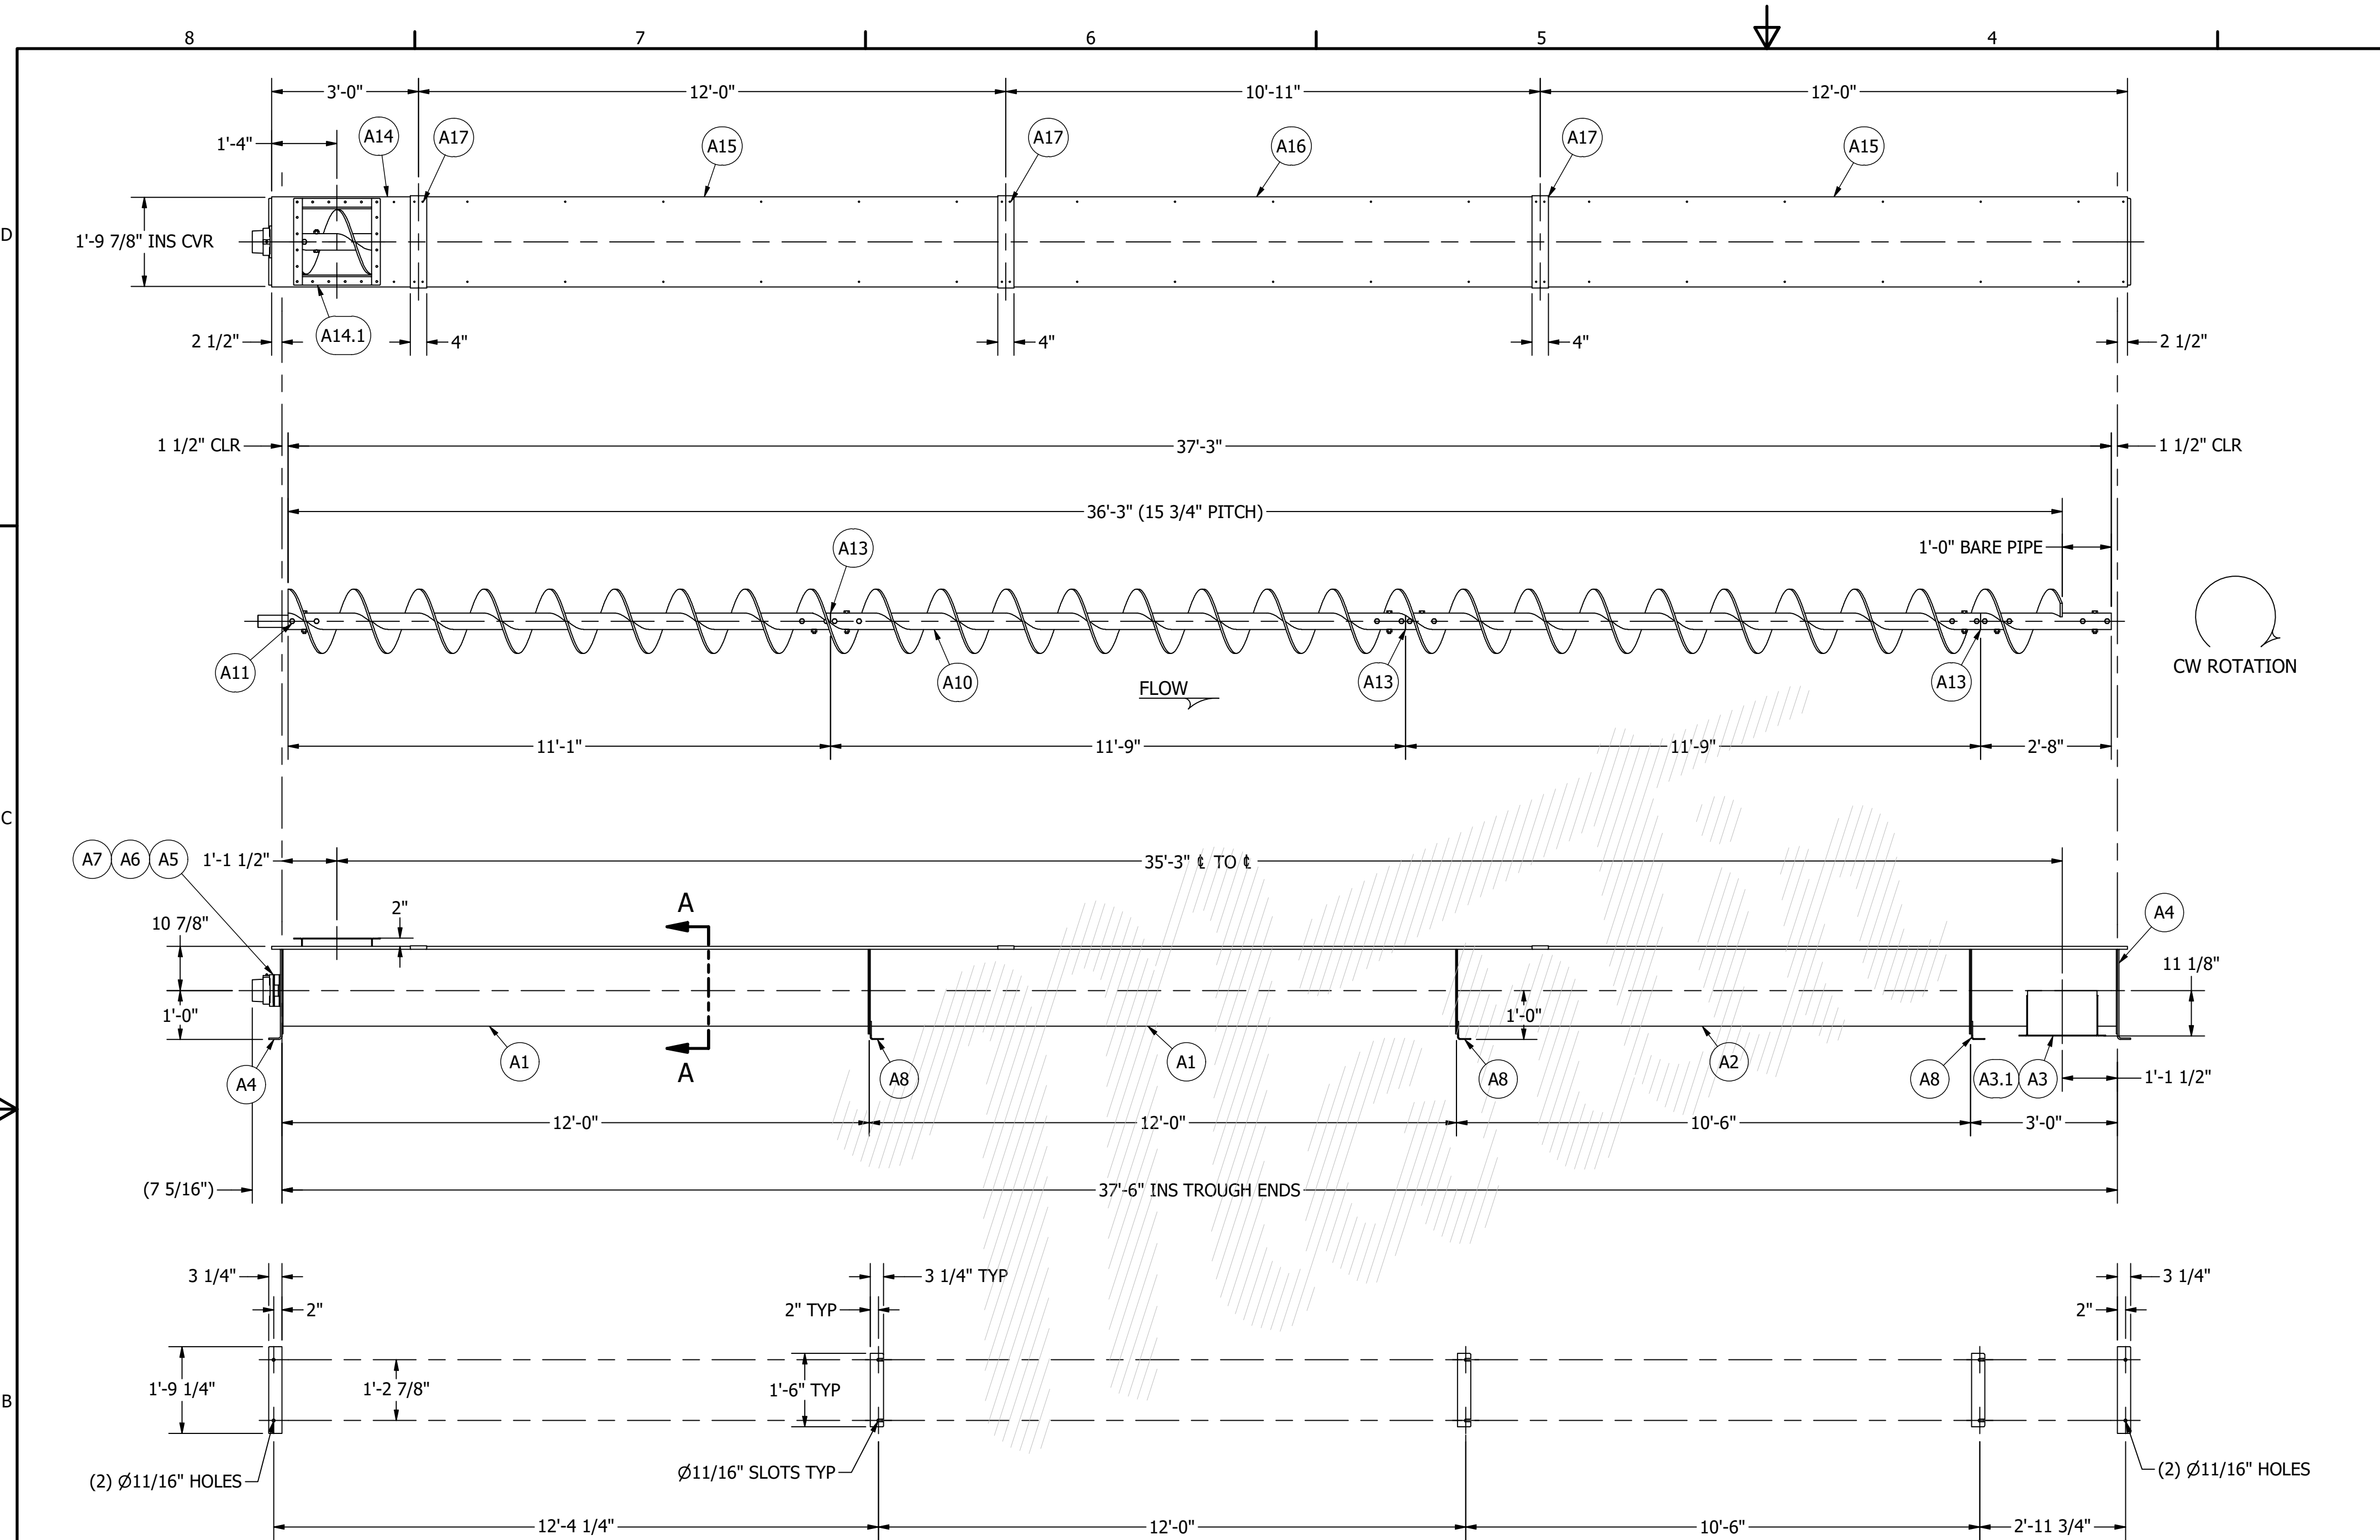


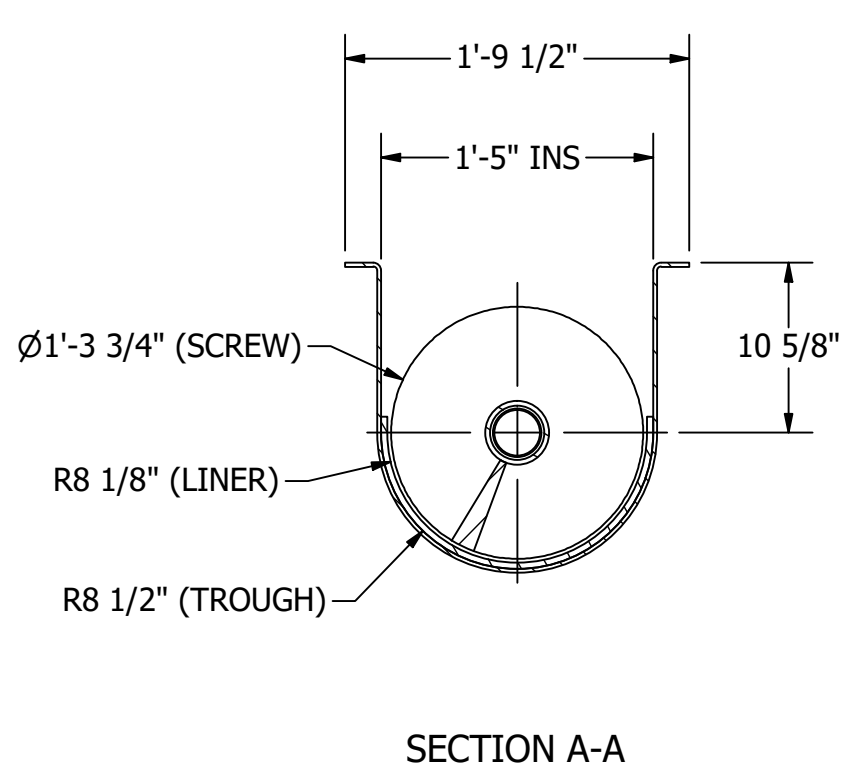

NOTES:
1. FOR SAFETY STICKER LOCATIONS, REFER TO CEMA SAFETY LABELS PLACEMENT GUIDE #SC-2
2. ONE (1) LOT OF STANDARD SHOP COAT OF WATER BASED GRAY ENAMEL PAINT - **EXTERIOR ONLY**
SHOP TO ASSEMBLE CONVEYOR WITH NO DRIVE INCLUDED

LUBRICATION LEVELS IN THE DRIVE REDUCER AND BEARINGS MUST BE VERIFIED PRIOR TO OPERATION

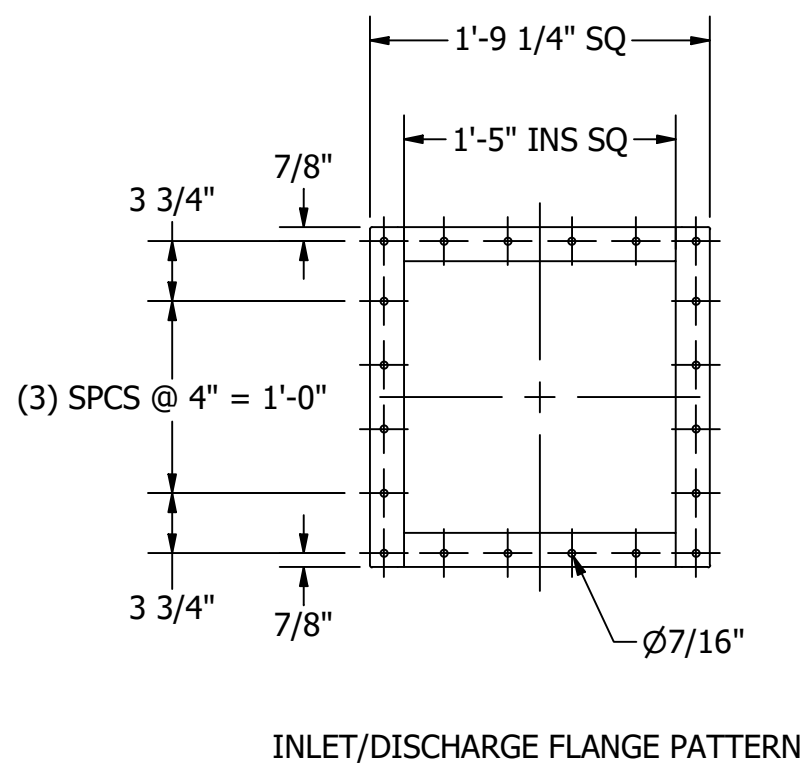

FOR APPROVAL
CONSTRUCTION IS BEING HELD

☐ APPROVED AS SUBMITTED
PROCEED WITH MANUFACTURING

☐ REVISE AND RESUBMIT FOR APPROVAL
DO NOT PROCEED WITH MANUFACTURING

PRINT NAME: _____
SIGNATURE: _____
COMPANY: _____
DATE: _____

PLEASE NOTE:
PRICING IS SUBJECT TO CHANGE DUE TO DESIGN CHANGES
OR MATERIAL VOLATILITY. THIRD-PARTY SUPPLIED ITEMS
ARE QUOTED BASED ON CURRENT AVAILABILITY, AND
MAY BE SUBJECT TO CHANGE BEFORE SHIPMENT

A	ISSUED FOR APPROVAL	DHL	6/18/2025
REV	DESCRIPTION	APPR	DATE
REVISION HISTORY			

THIS DRAWING AND DESIGN IS CONFIDENTIAL. THE RETURN OF THIS DRAWING MAY BE REQUIRED UPON DEMAND. NEITHER THIS DRAWING NOR DESIGN MAY BE COPIED WITHOUT EXPRESSED AUTHORIZATION FROM *Martin* SPROCKET & GEAR, INC.

BILL OF MATERIALS						
RSP	ITEM	ITEM QTY	PART NUMBER	MATERIAL	DESCRIPTION	DETAIL
	A	1	SC-16		16" X 37' 6" LONG CARBON STEELSCREW CONVEYOR PAINTED GRAYCONVEYOR IS SHOP ASSEMBLED WITH NO DRIVE INCLUDED ON A 15 DEG INCLINE	
	A1	2	0790962M-TRGH1	Steel, Mild	16" U-SHAPE TROUGH, 12' 0" O.A.L., CONSTRUCTED FROM 1/4" THK CARBON STEEL MATERIAL FITTED WITH 3/8" THICK AR225 TROUGH LINER, LINER TO BE 1" ABOVE CENTERLINE AND STITCH WELDED IN PLACE	
	A2	1	0790962M-TRGH2	Steel, Mild	16" U-SHAPE TROUGH, 10' 6" O.A.L., CONSTRUCTED FROM 1/4" THK CARBON STEEL MATERIAL FITTED WITH 3/8" THICK AR225 TROUGH LINER, LINER TO BE 1" ABOVE CENTERLINE AND STITCH WELDED IN PLACE	
	A3	1	0790962M-TRGH3	Steel, Mild	16" U-SHAPE TROUGH, 3' 0" O.A.L., CONSTRUCTED FROM 1/4" THK CARBON STEEL MATERIAL FITTED WITH STD 16TSD7, 3/16" THK DISCHARGE, LOCATED 13 1/2" ON CENTER FROM DISCHARGE END. FITTED WITH 3/8" THICK AR225 TROUGH LINER, LINER TO BE 1" ABOVE CENTERLINE AND STITCH WELDED IN PLACE	
	A3.1	1	16TSD7	Steel, Mild	16" X 3/16" THK. DISCHARGE SPOUT FITTED	
	A4	2	16TEF6-BB-P	Steel, Mild	16" X 3" TROUGH END	
**	A5	1	TEB6BB		3" FLANGE BALL BEARING (#126197)	
	A6	1	EC-216		3" DODGE CLOSED END CLOSURE SNAP-ON END COVER (#128222)	
**	A7	1	CSW6	Steel, Mild	3" WASTE PACK SEAL W/ PACKING	
	A8	3	16TFF	Steel, Mild	16" FLANGE FOOT	
	A9	1	CAULK LATEX		CAULK; LATEX	
	A10	1	0790962M-SCREW1	Steel, Mild	STARTING AT INLET END 1ST 36' 3" TO BE 15 3/4" O.D. X 16" PITCH X 1/2" THK RIGHT HAND CARBON STEEL SECTIONAL FLIGHTS LAST 1' TO BE BARE PIPE CONTINUOUSLY WELDED BOTH SIDES WITH A CEMA II WELD FINISH TO A 3 1/2" CARBON STEEL SCH. 80 PIPE BOTH ENDS BUSHED & 3-BOLT DRILLED FOR A 3" COUPLING CLOSE COUPLED & Clocked TO MAKE TOTAL O.A.L. OF 37' 3" SCREW LENGTHS IN SEQUENCE FROM INLET AS: 11' 1", 11' 9", 11' 9" AND 2' 8" MARTIN RECOMMENDS THE USE OF TROUGH LINERS AND HOLD DOWN ANGLES WITH CLOSE COUPLED & Clocked SCREWS	
**	A11	24	CCB6	Steel, Mild	Ø3/4" X 5" GRADE 2 COUPLING BOLT W/ LOCKNUT	
	A12	1	CE6BB-W-3	Steel, Mild	3" DIA. X 15 3/8" LG. END SHAFT, 3-BOLT	
**	A13	3	CCC6-3	Steel, Mild	3" DIA CLOSE COUPLING SHAFT, 3-BOLT	
	A14	1	0790962M-CVR1	Steel, Mild	NOM 16" FLANGED TROUGH COVER X 3' O.A.L. 21 7/8" WIDE TO FIT OVER STD TROUGH TOP RAILS, CONSTRUCTED FROM 12GA THK CARBON STEEL MATERIAL, BOLTED ON 2'-0" CENTERS, 3/16" THK INLET, LOCATED 16" ON CENTER FROM COVER EDGE	
	A14.1	1	16CIF	Steel, Mild	16" FIXED INLET	
	A15	2	16TCF12-12-H	Steel, Mild	16" X 12GA X 12' LG FLANGED COVER, BOLTED ON 2'-0" CENTERS	
	A16	1	0790962M-CVR2	Steel, Mild	NOM 16" FLANGED TROUGH COVER X 10' 11" O.A.L. 21 7/8" WIDE TO FIT OVER STD TROUGH TOP RAILS, CONSTRUCTED FROM 12GA THK CARBON STEEL MATERIAL, BOLTED ON 2'-0" CENTERS	
	A17	3	16BLF10	Steel, Mild	16" X 4" FORMED FLANGED U-TROUGH BUTT STRAP	
	A18	82'	SP150		1/8" X 1 1/2" BLACK SPONGE GASKET	
	A19	8'	SP400		1/8" X 4" BLACK SPONGE GASKET	
	A20	A/R	ASSEMBLY BOLTS	Steel, Mild	LOT OF ASSEMBLY BOLTS	
	A21	1	MH-TAG	Aluminum	MH NAME PLATE	

**RECOMMENDED SPARE PARTS

ALL SCREW DIAMETERS AND PITCH TOLERANCES PER CEMA STANDARDS (ACCORDING TO SIZE). ALL TOLERANCES TO CONFORM TO PUBLISHED MARTIN OR CEMA STANDARDS. ALL OTHERS AS FOLLOWS:		ORIGINAL BRANCH	18	<i>Martin</i> SPROCKET AND GEAR, INC.	3600 McCART AVE FORT WORTH, TX 76110-4692 PH.: 817-258-3000 FAX: 817-258-3173 WEB SITE: www.martinsprocket.com	
• ANGULAR: +/- 1° • HOLE DIAMETERS: +/- .132" • DECIMAL: TWO PLACES +/- .06" • THREE PLACES +/- .005" • FRACTIONAL: UNDER 12" +/- 1/16" 12" TO 120" +/- 1/8" 120 AND OVER +/- 1/4"		CUSTOMER: A GLADE DYESS SALES 540 MOONRISE ST WAXAHACHIE, TX 75165 USA		DESCRIPTION: MTSCREW CONVEYOR		
MACHINED SURFACES: 125√		TAG NO.		20313073		
3RD ANGLE PROJECTION		CUST. P.O.		05272025TGD		
S.O. NO.:		S02503205		PART NO.		SC-16
EST. WEIGHT	DRAWN	DRAW DATE	CHECKED	CHECK DATE	SCALE	PRINT NUMBER
4841.56 lbs	RMI	6/16/2025	DHL	6/18/2025	NTS	0790962M
					SHEET	1 of 1
					REV	A