


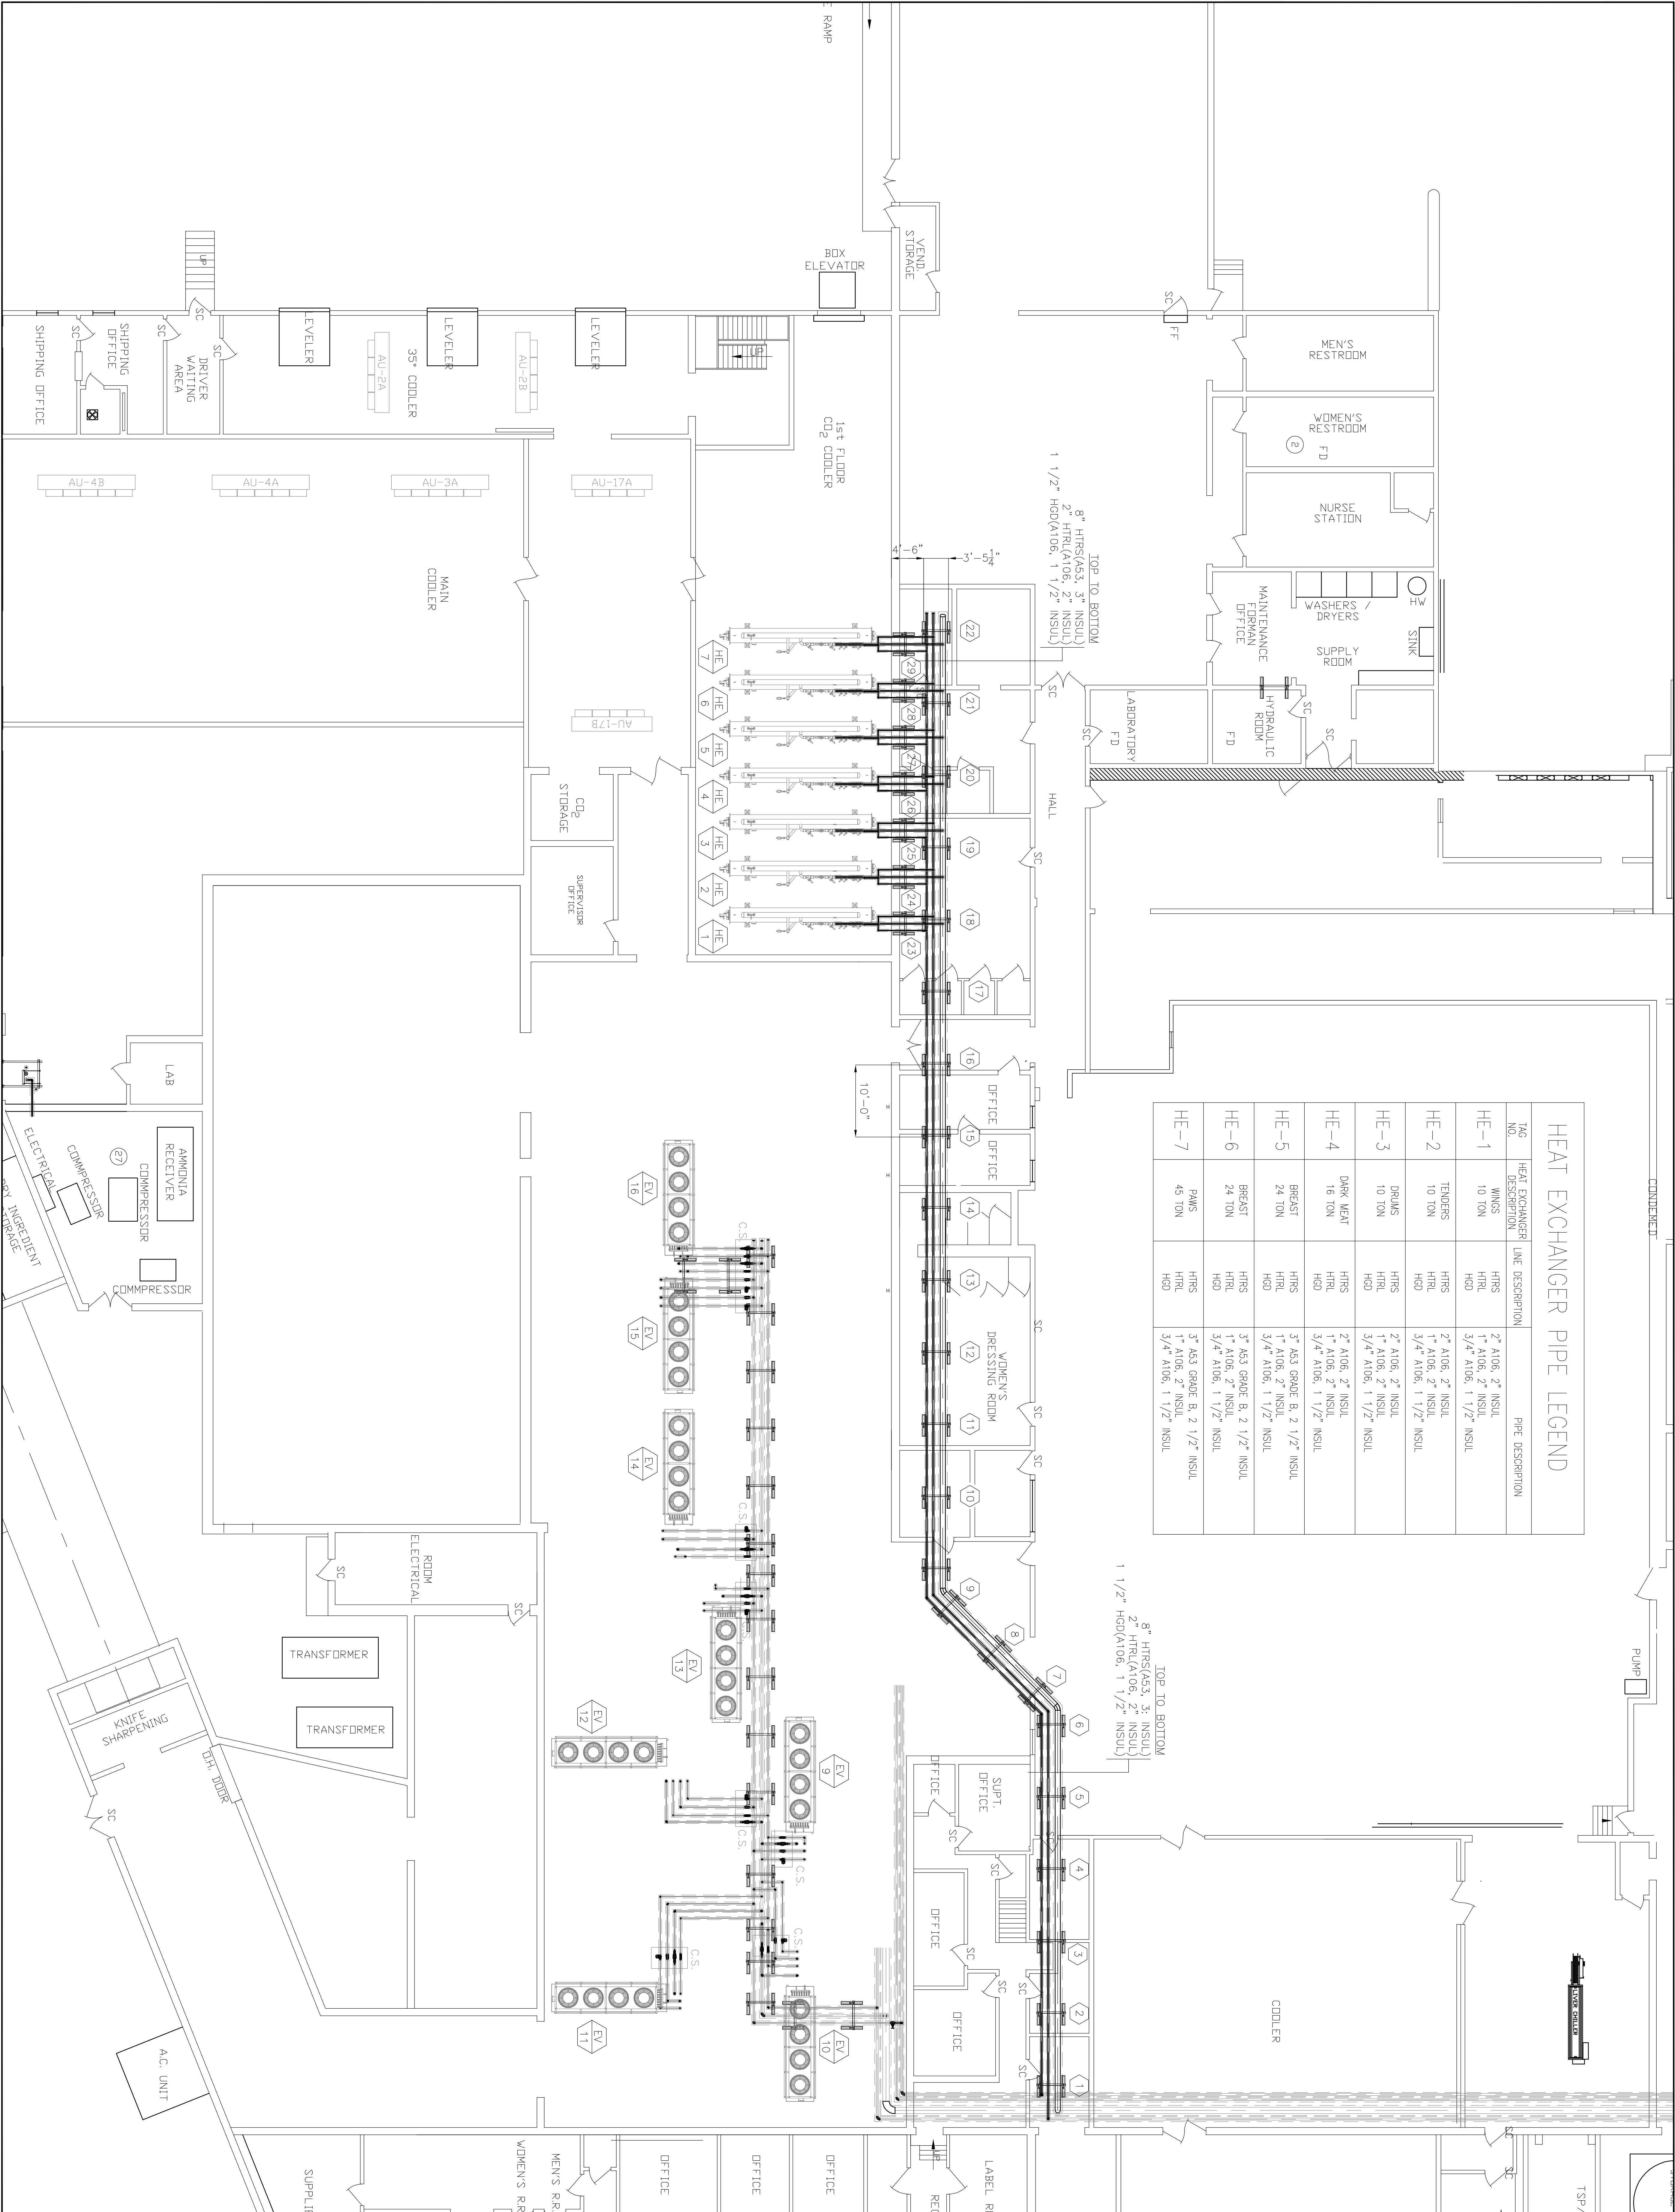

HEAT EXCHANGER PIPE LEGEND		
TAG NO.	HEAT EXCHANGER DESCRIPTION	PIPE DESCRIPTION
HE-1	WINGS 10 TON	2" A106, 2" INSUL 1" A106, 2" INSUL 3/4" A106, 1 1/2" INSUL
HE-2	TENDERS 10 TON	2" A106, 2" INSUL 1" A106, 2" INSUL 3/4" A106, 1 1/2" INSUL
HE-3	DRUMS 10 TON	2" A106, 2" INSUL 1" A106, 2" INSUL 3/4" A106, 1 1/2" INSUL
HE-4	DARK MEAT 16 TON	2" A106, 2" INSUL 1" A106, 2" INSUL 3/4" A106, 1 1/2" INSUL
HE-5	BREAST 24 TON	3" A53 GRADE B, 2 1/2" INSUL 1" A106, 2" INSUL 3/4" A106, 1 1/2" INSUL
HE-6	BREAST 24 TON	3" A53 GRADE B, 2 1/2" INSUL 1" A106, 2" INSUL 3/4" A106, 1 1/2" INSUL
HE-7	PANS 45 TON	3" A53 GRADE B, 2 1/2" INSUL 1" A106, 2" INSUL 3/4" A106, 1 1/2" INSUL

CR2504H

7/13/25

R4.0

DRAWING DESCRIPTION

FLOOR PLAN PIPE LAYOUT

WAYNE FARMS UNION SPRINGS, AL

Republic Refrigeration, Inc.

2810 Gray Fox Road Monroe, NC 28110 [704] 282-0399

SCALE

DESIGNED BY

DRAWN BY

CHECKED BY

REVISIONS

NO.	DESCRIPTION	BY
1	3/19/23 CHANGED PIPING ON EV-15/ EV-16	