


VALVE LEGEND	
TAG NO.	LINE IDENT. VALVE DESCRIPTION
A	HTRS 1" PORT HANSEN HA4D REGULATOR
B	HTRL 1" PORT HANSEN HS4A SOLENOID, STRAINER
C	HGD 3/4" PORT HANSEN HS7 SOLENOID, STRAINER
D	RV HANSEN HS632, 250# DUAL RELIEF VALVE ASSEMBLY

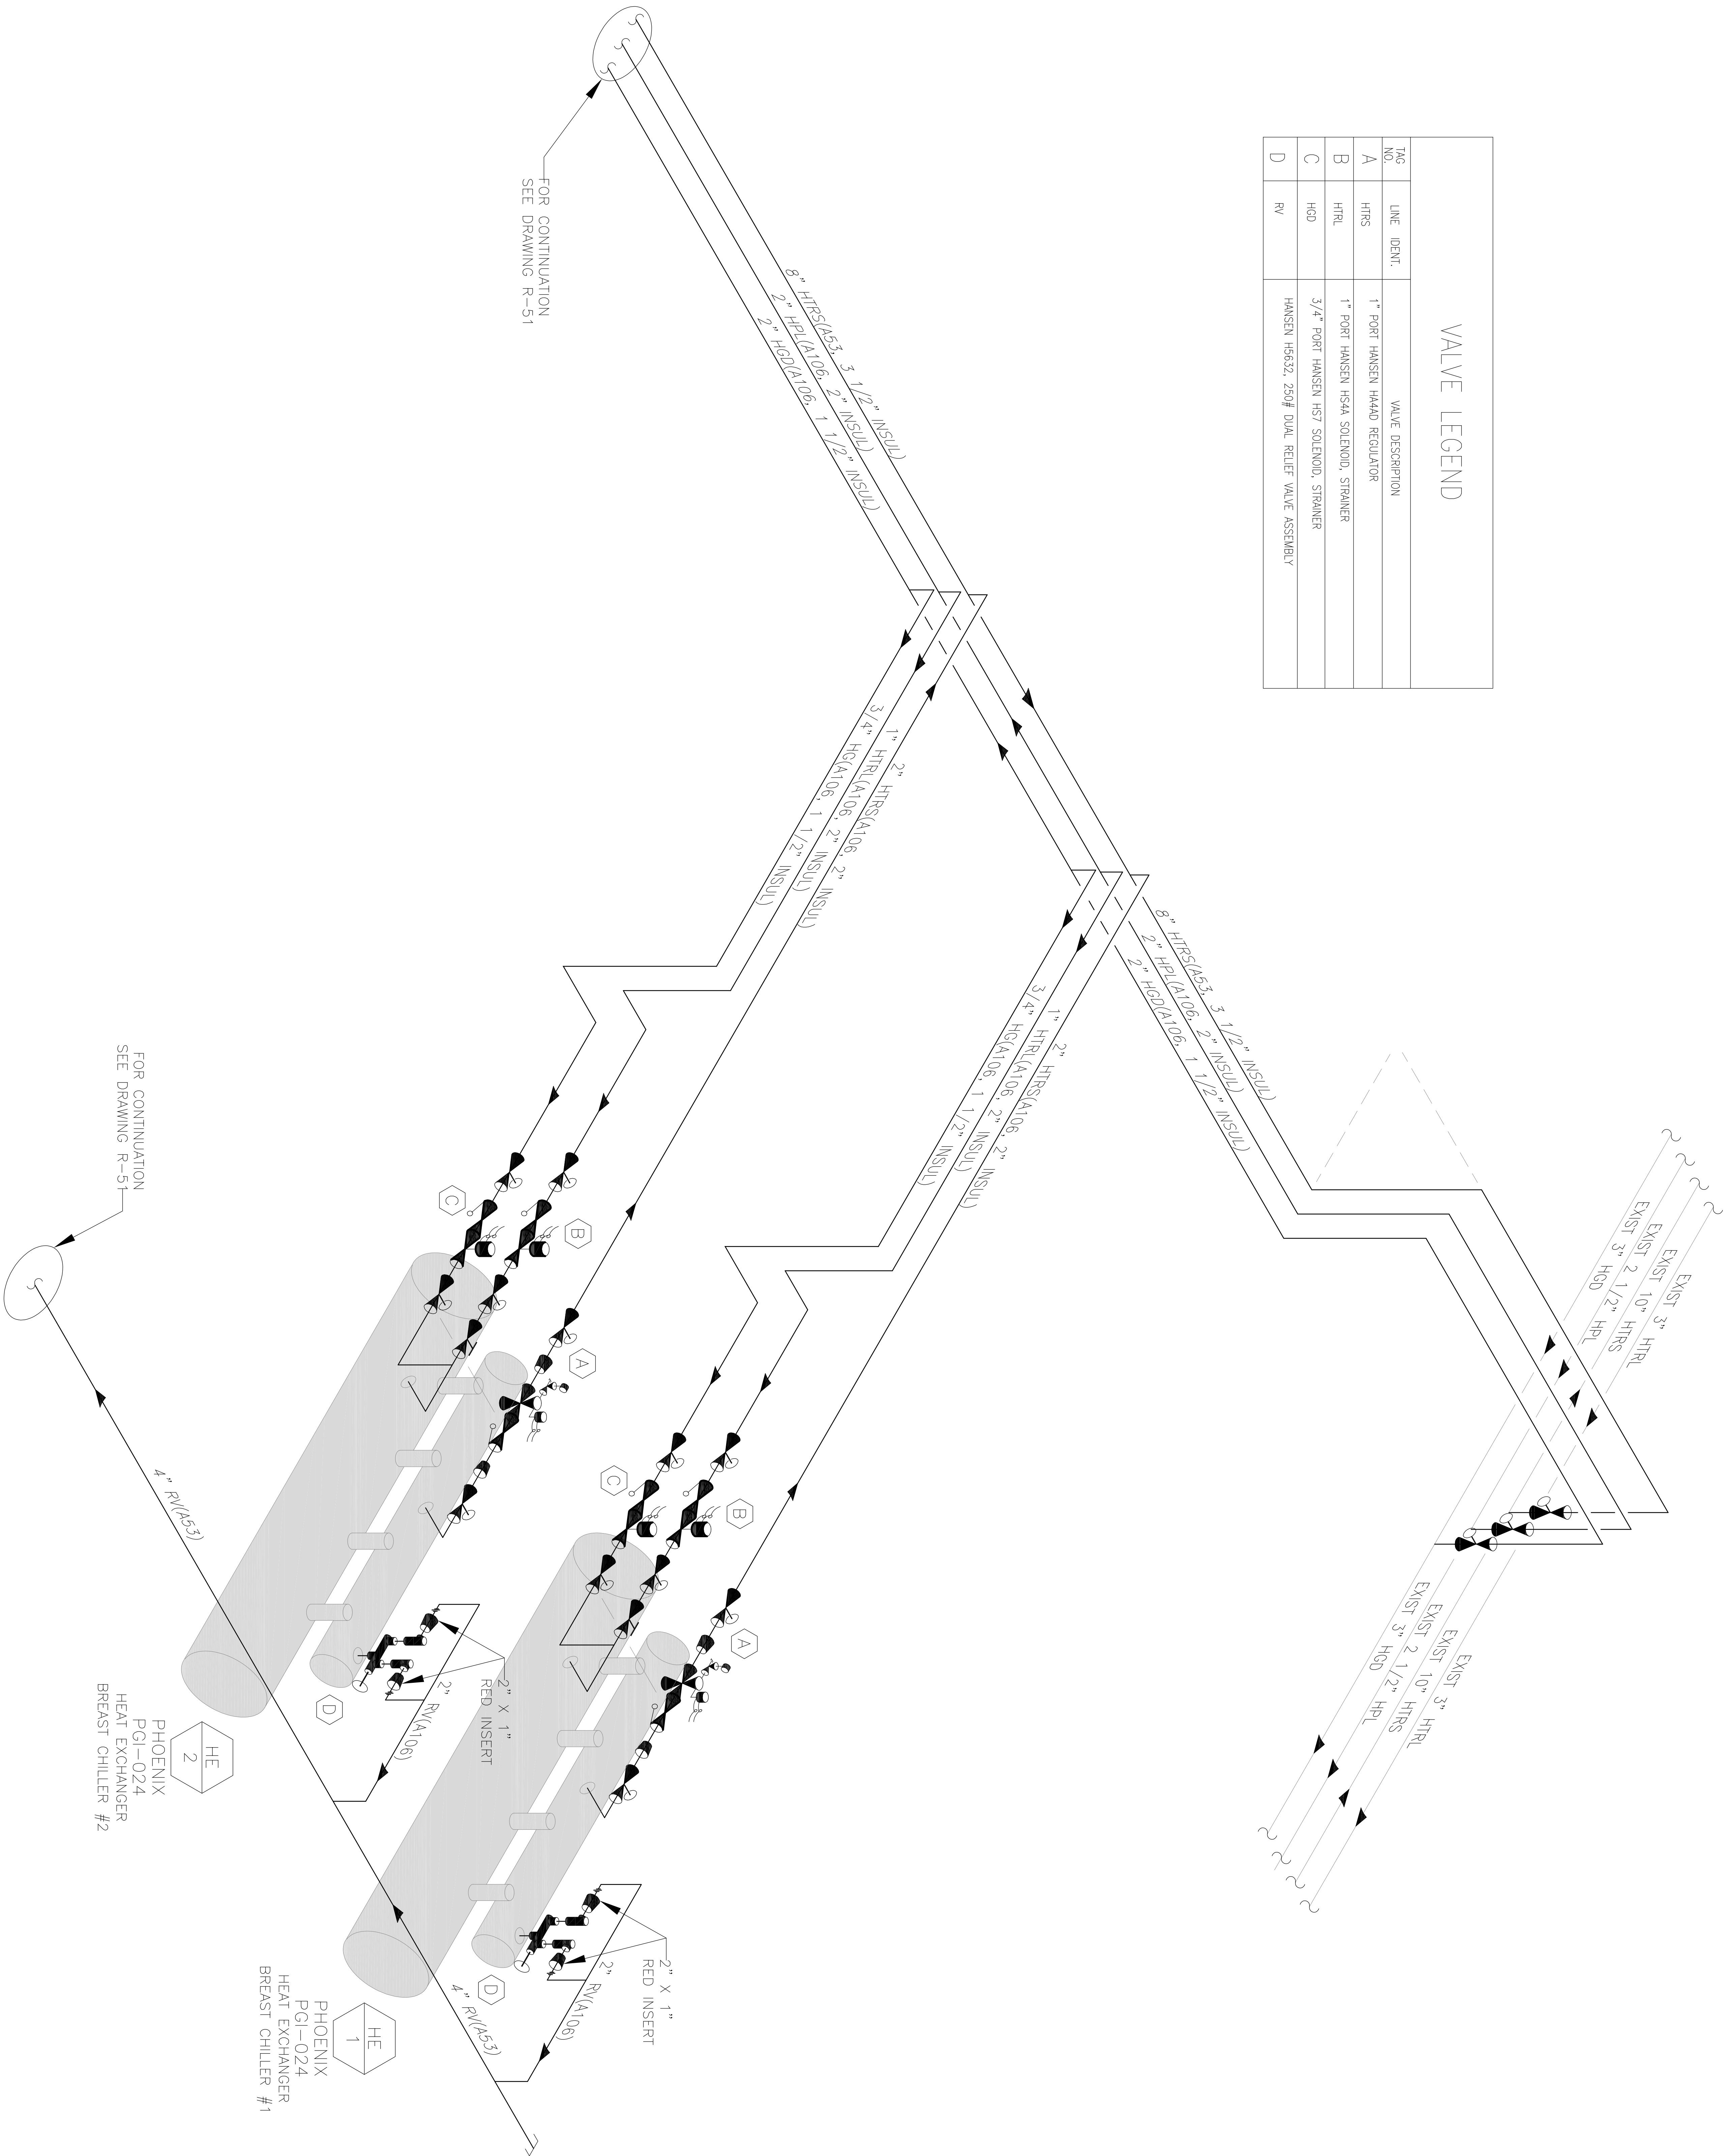

CR2504H	PROJECT NO.	DATE 9/20/25	DRAWING R-50	ISOMETRIC HEAT EXCHANGERS	DRAWING DESCRIPTION WAYNE SANDERSON FARMS UNION SPRINGS, AL	Republic Refrigeration, Inc. 2810 Gray Fox Road Monroe, NC 28110 [704] 282-0399	SCALE			REVISIONS		
							DESIGNED BY			NO.	DESCRIPTION	BY
							DRAWN BY					
							CHECKED BY					