




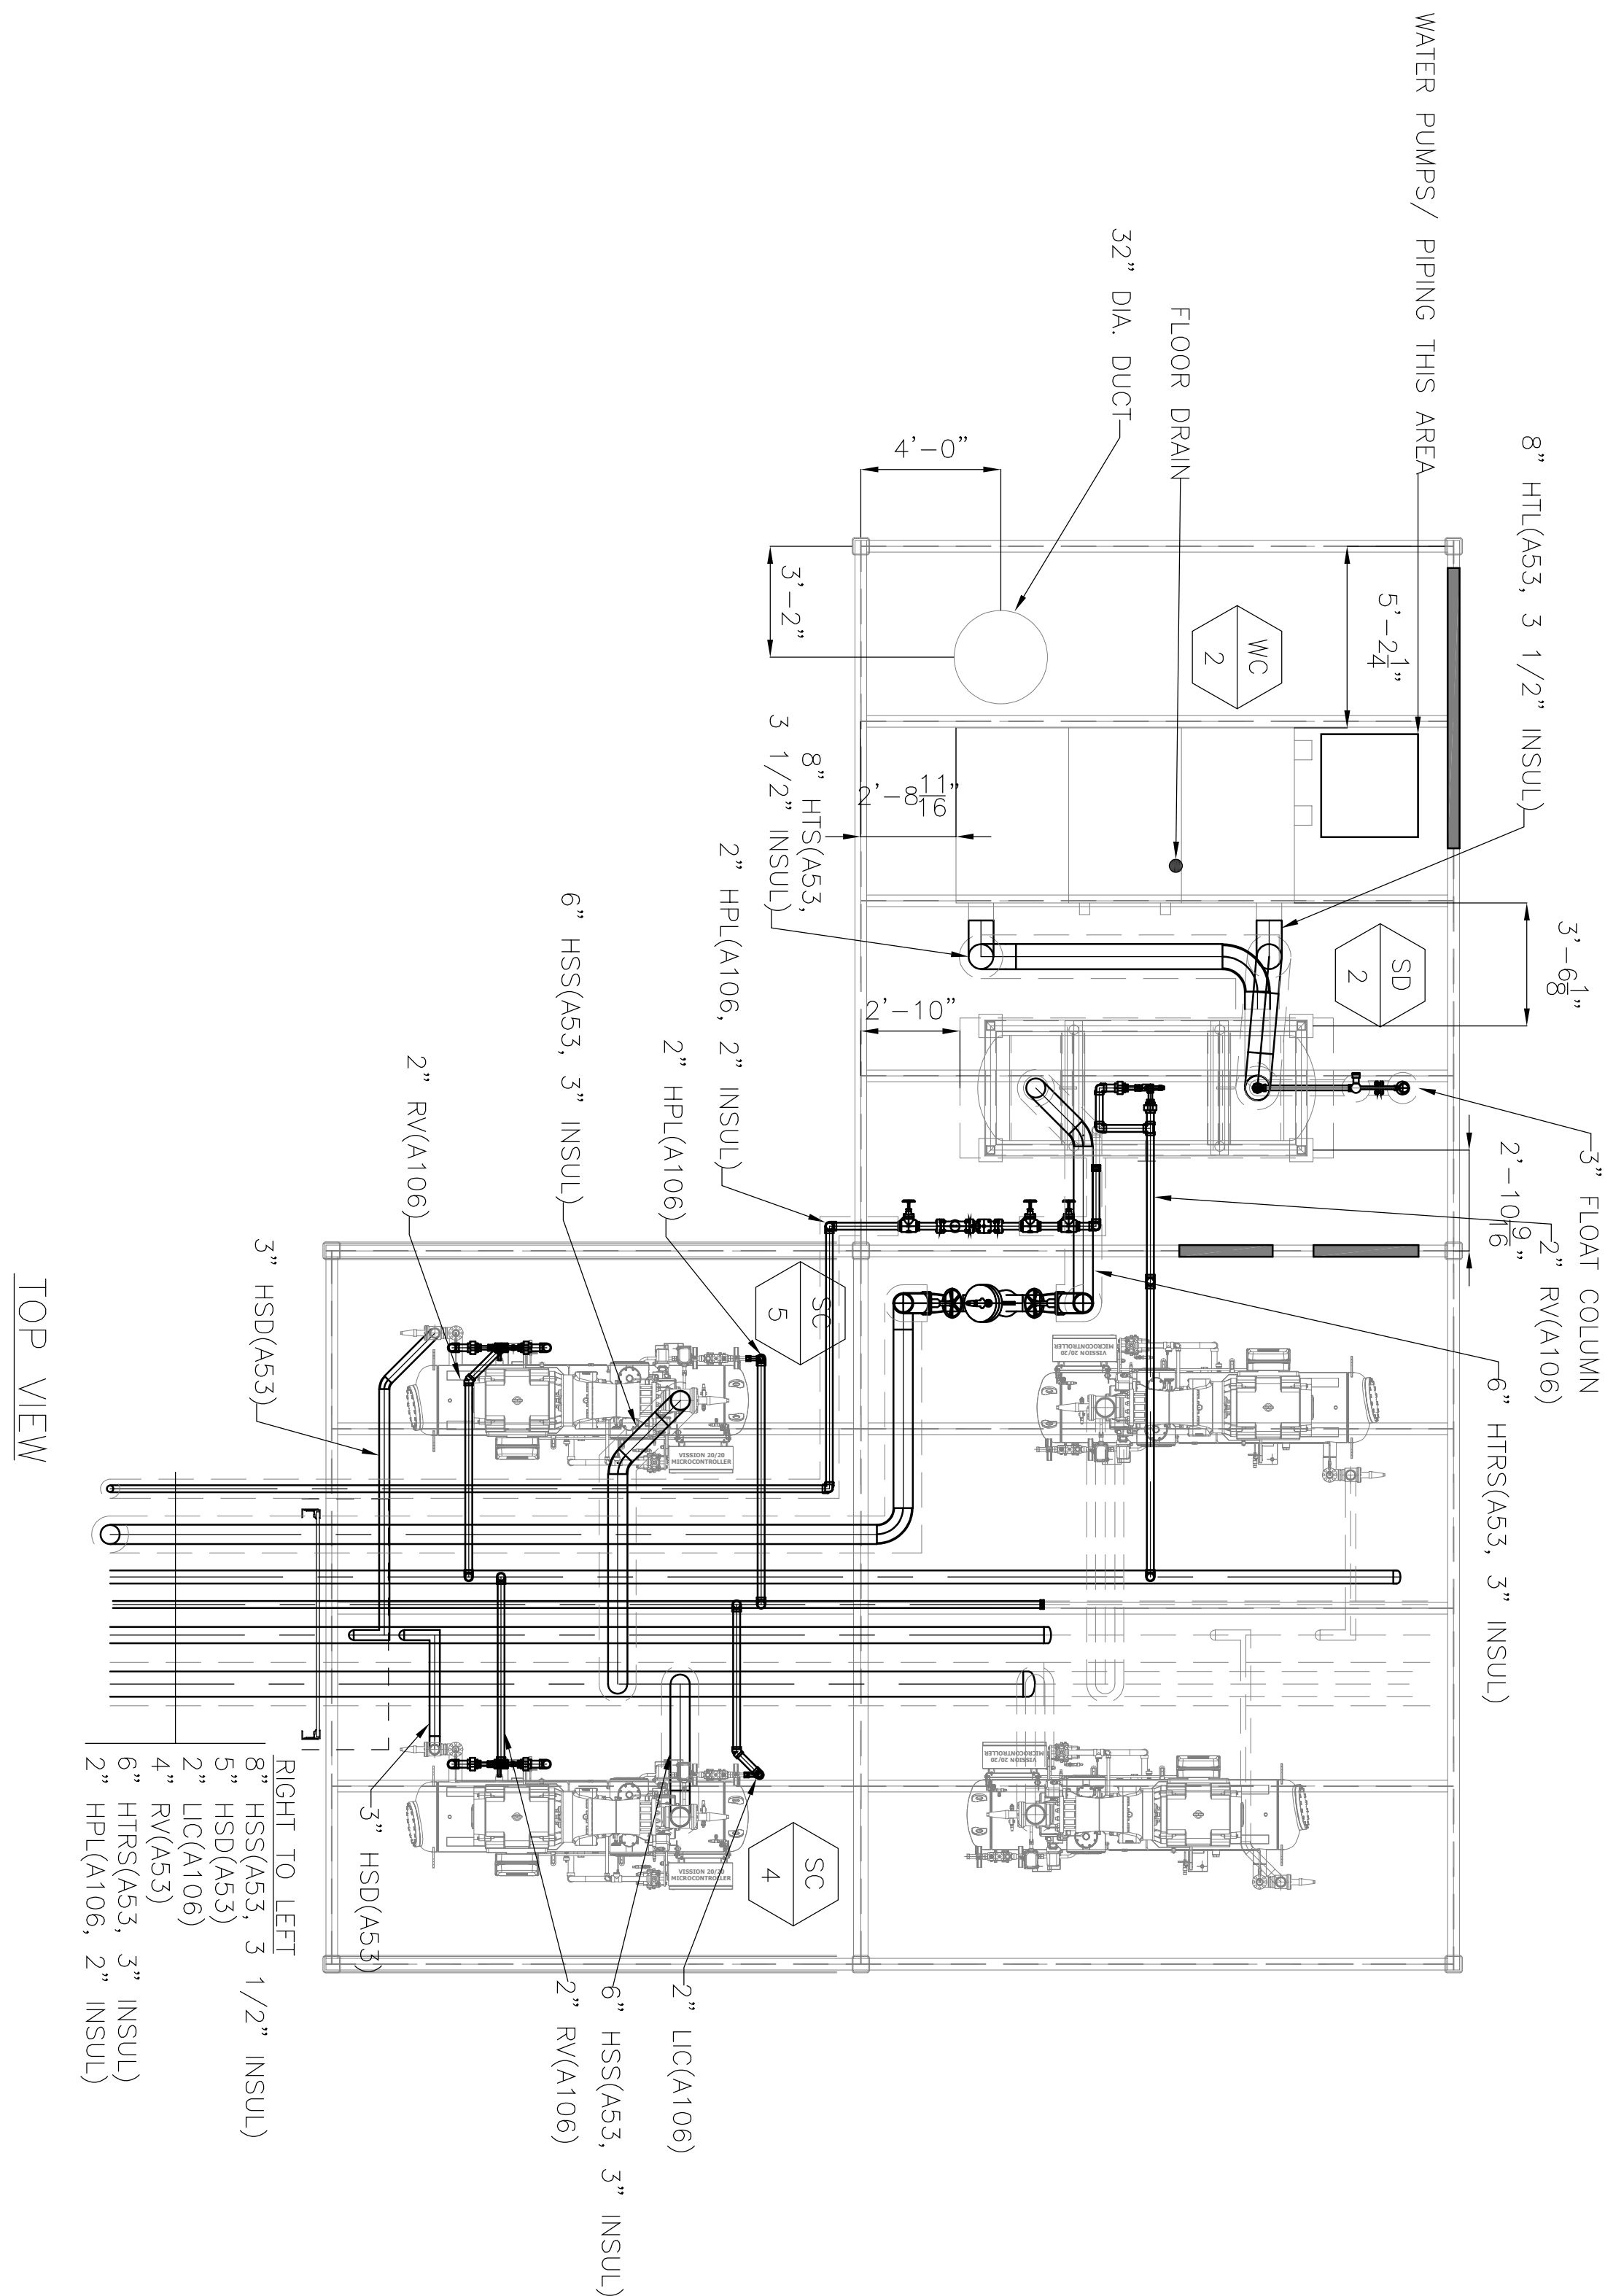

TOP VIEW

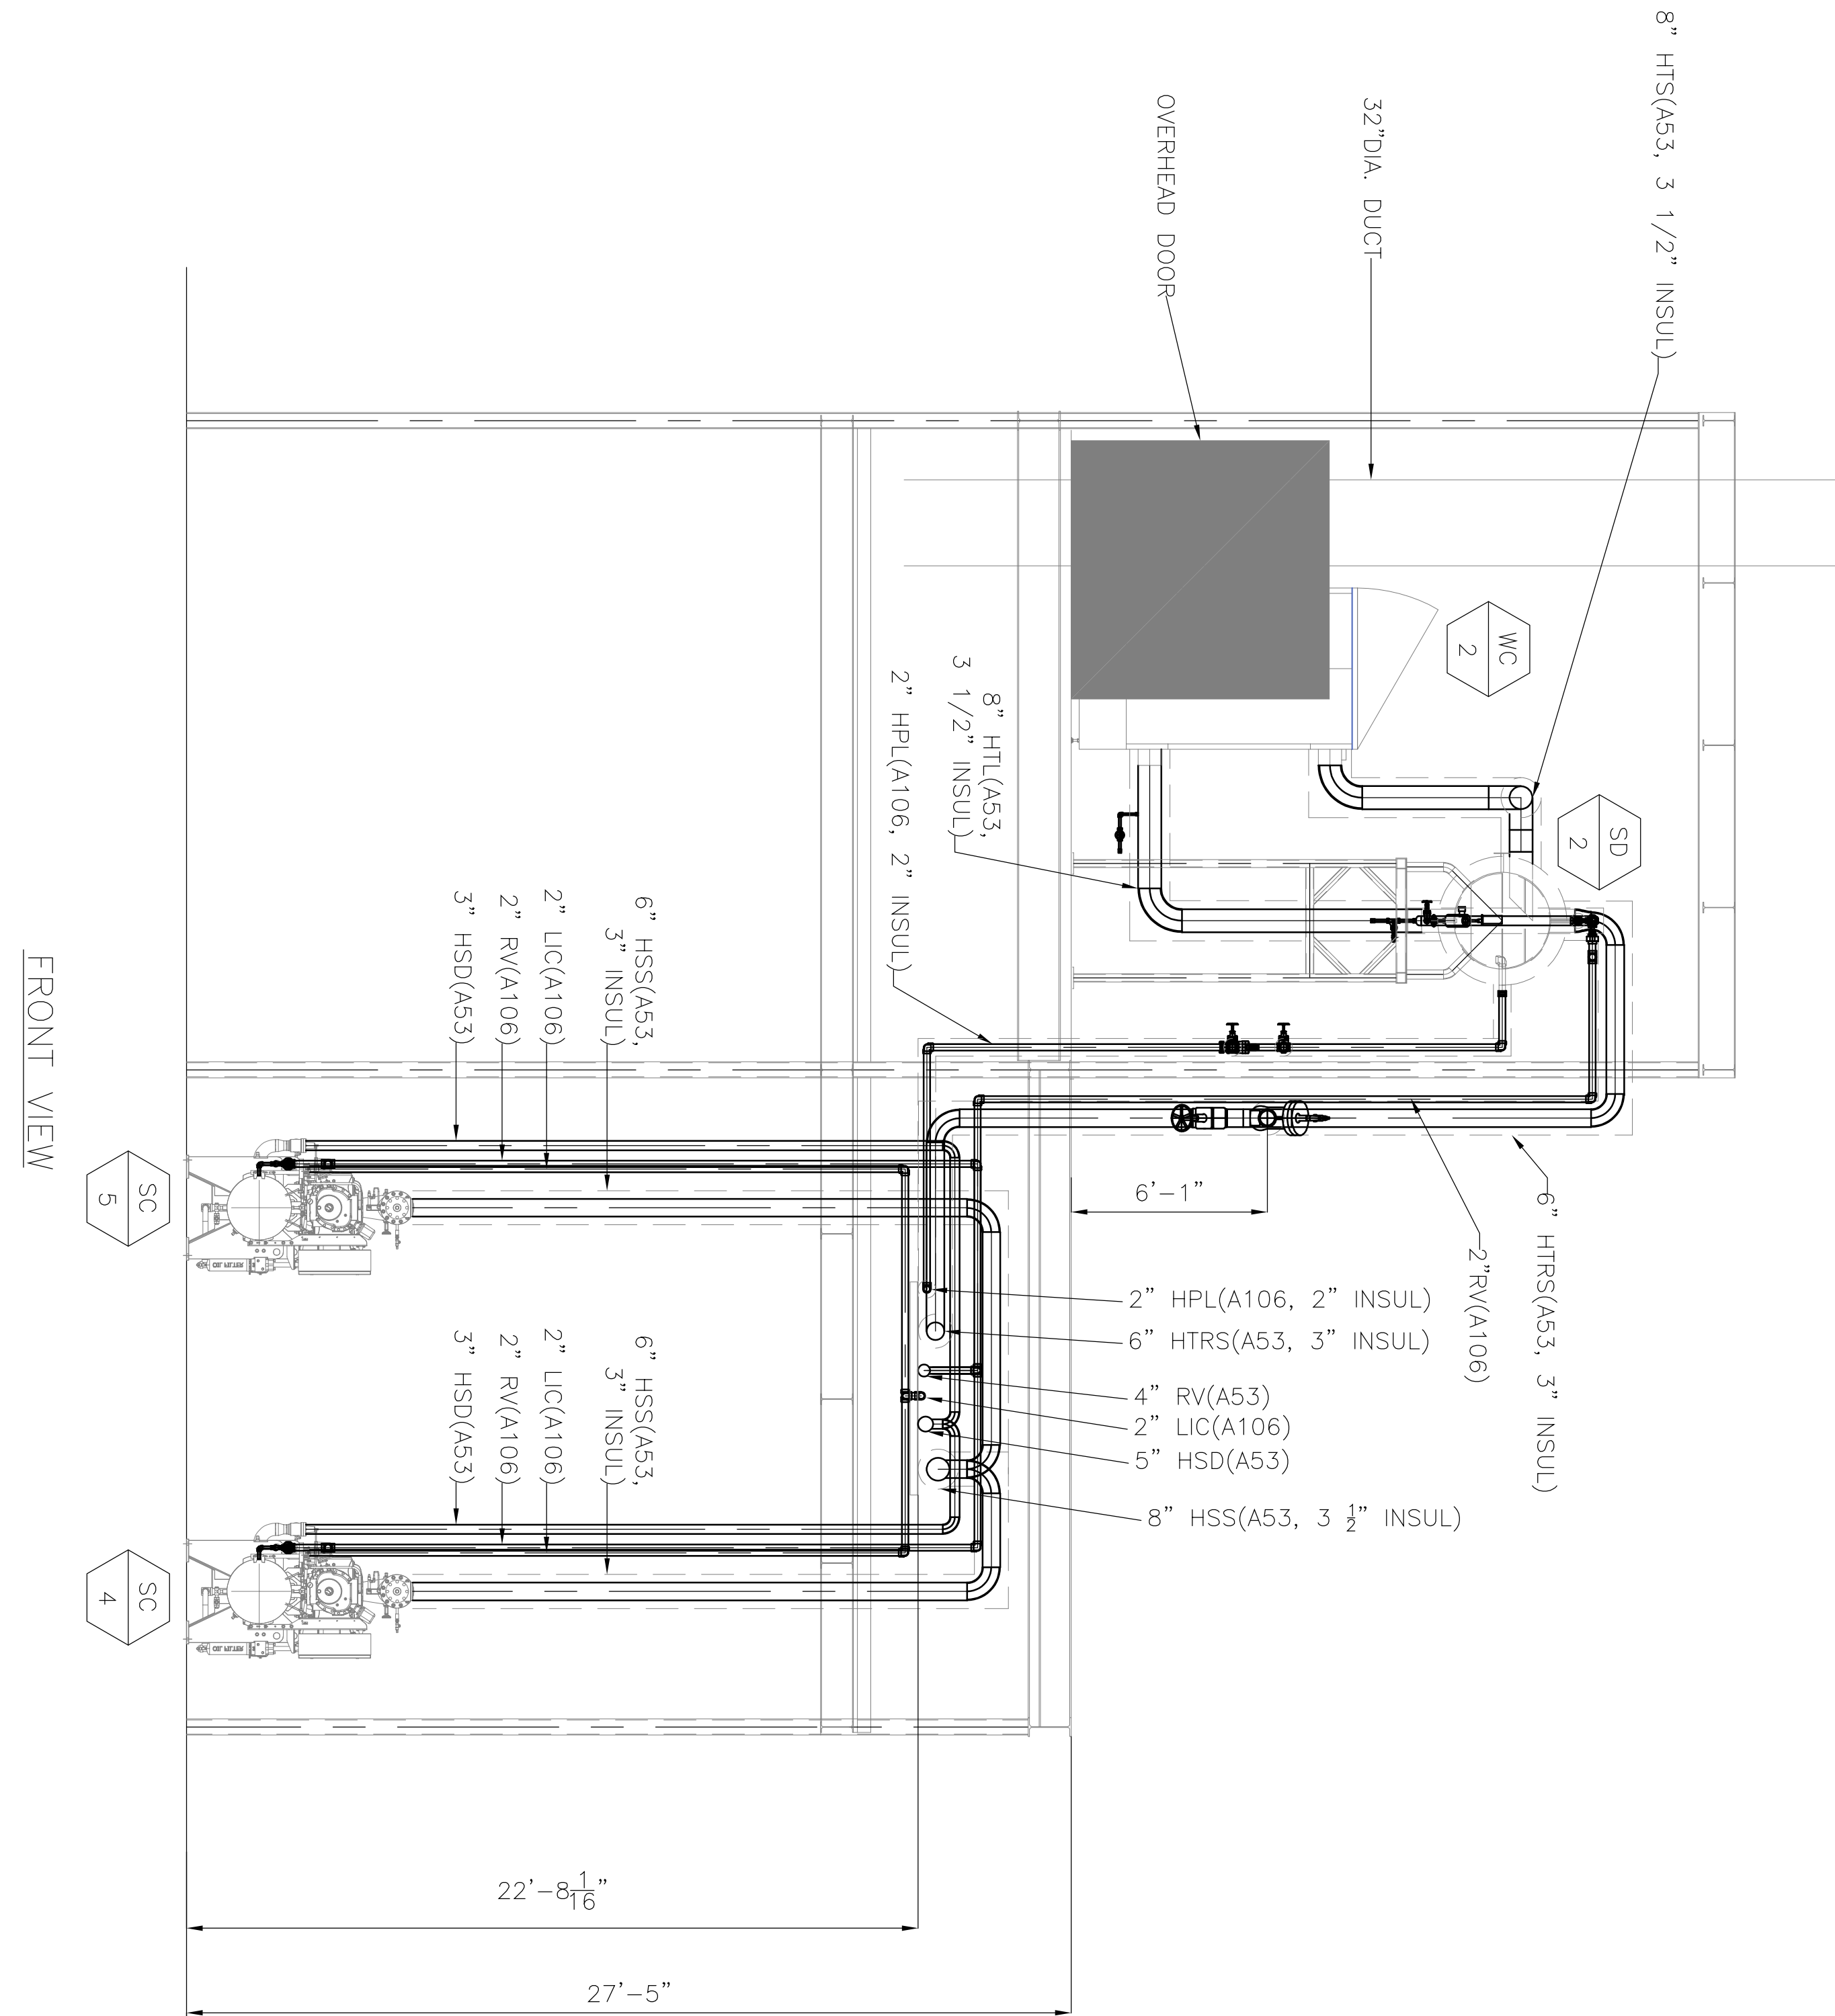

FRONT VIEW

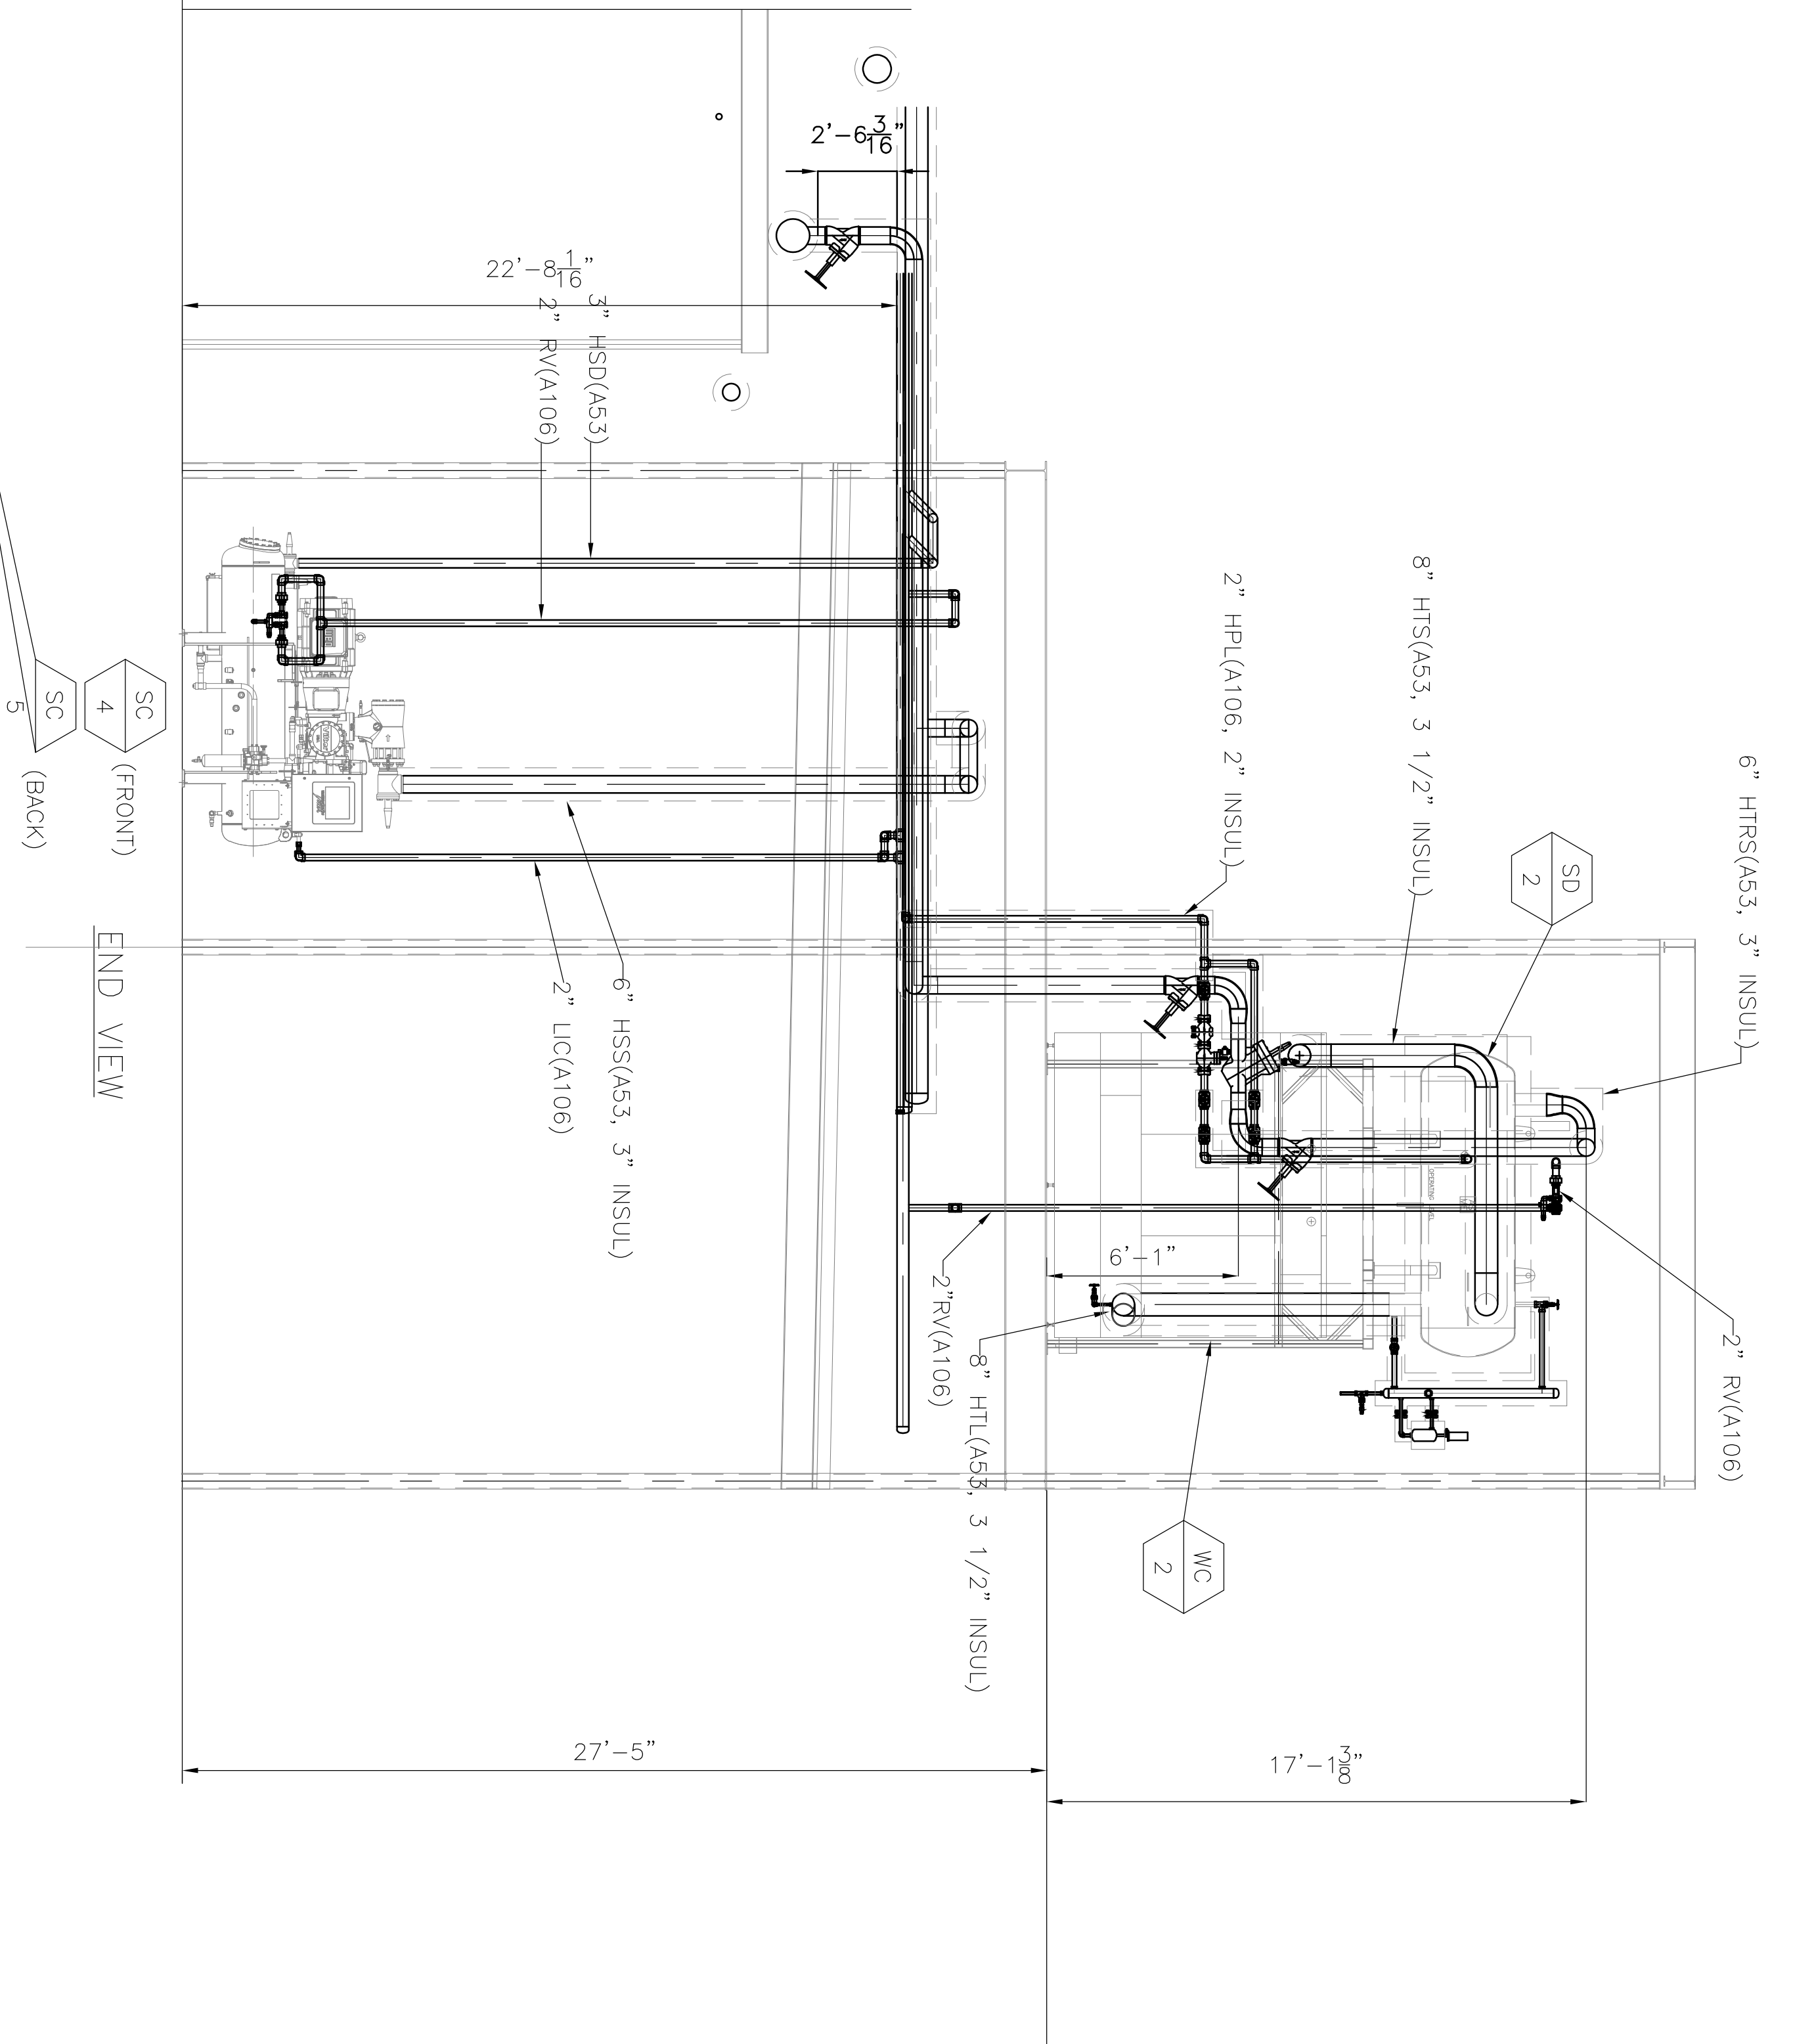

END VIEW

REVISIONS			
NO.	DESCRIPTION	BY	
X	X	X	X

SCALE	
DESIGNED BY	
DRAWN BY	JIM S
CHECKED BY	

Republic Refrigeration, Inc.

2810 Gray Fox Road Monroe, NC 28110

[704] 282-0399

WAYNE SANDERSON FARMS

UNION SPRINGS, AL

ENGINE ROOM
PIPING
DETAILS

R4.6

DATE
9/29/25

PROJECT NO.
CR2504M