


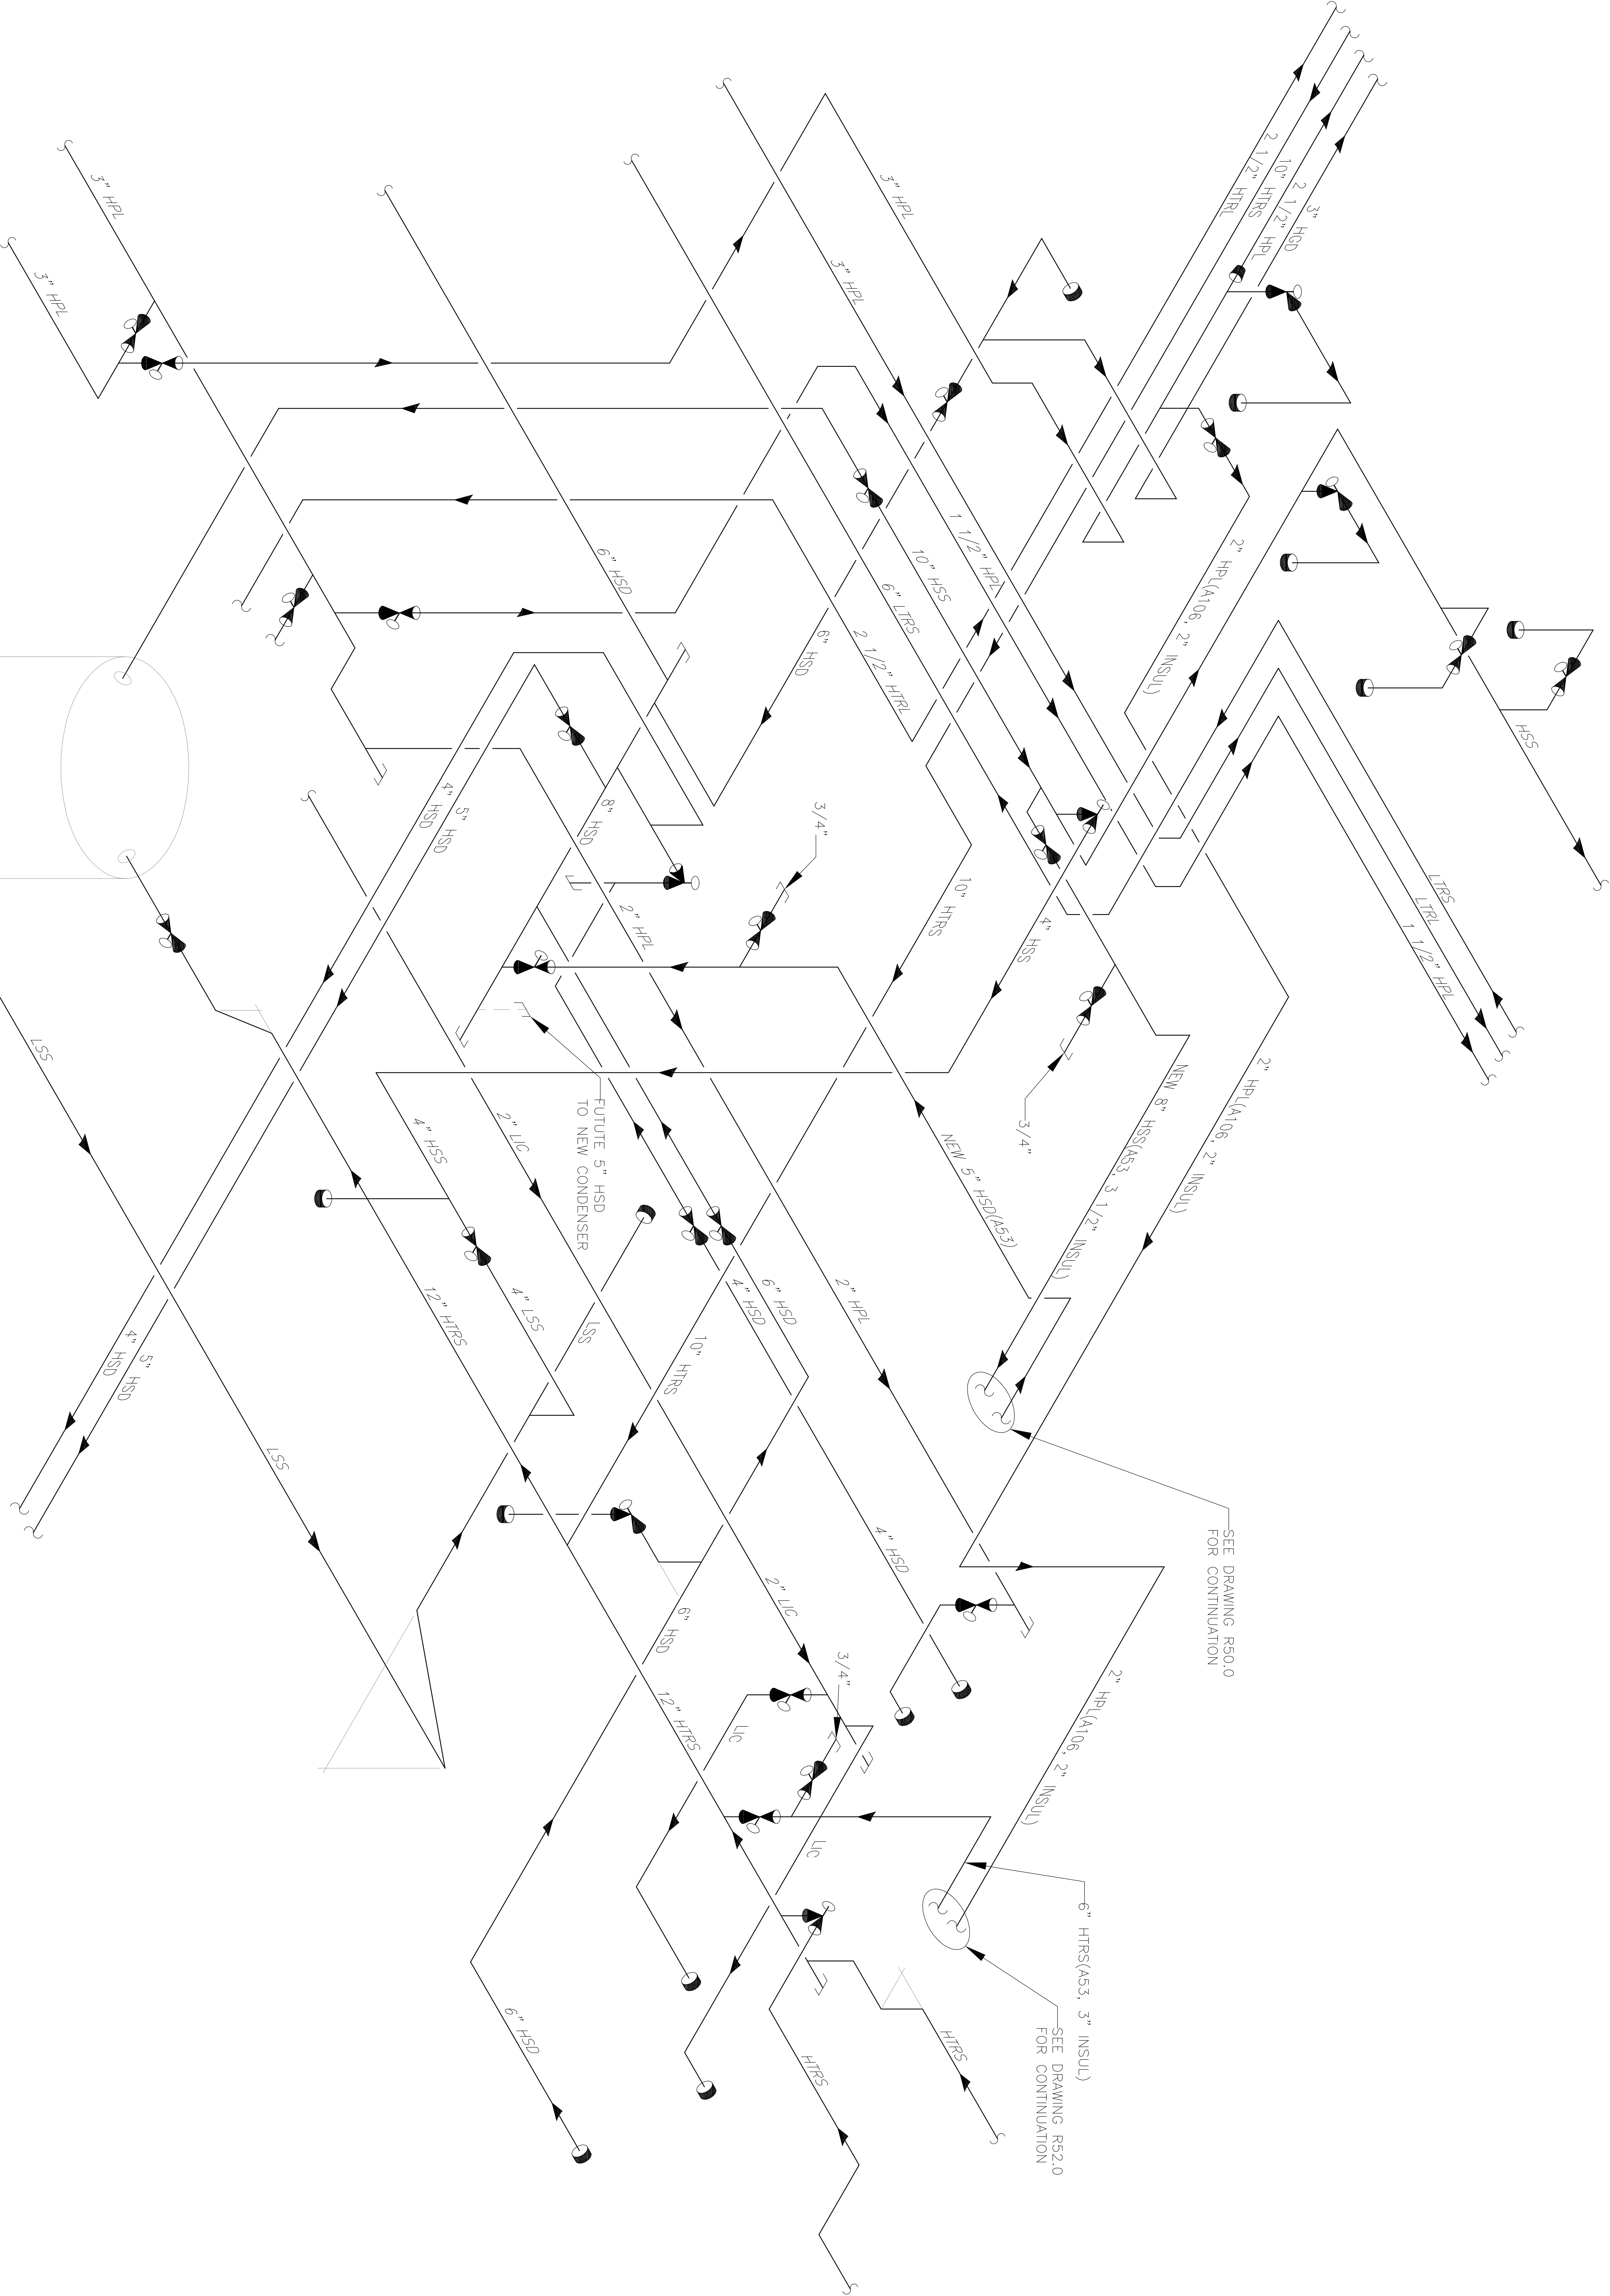

PROJECT NO. CR2504M		DATE 10/6/25		DRAWING R-51		ISOMETRIC ENGINE ROOM PIPING		DRAWING DESCRIPTION WAYNE SANDERSON FARMS UNION SPRINGS, AL		Republic Refrigeration, Inc. 2810 Gray Fox Road Monroe, NC 28110 [704] 282-0399		SCALE DESIGNED BY DRAWN BY JIM S CHECKED BY		REVISIONS NO. DESCRIPTION		BY	
														X		X	