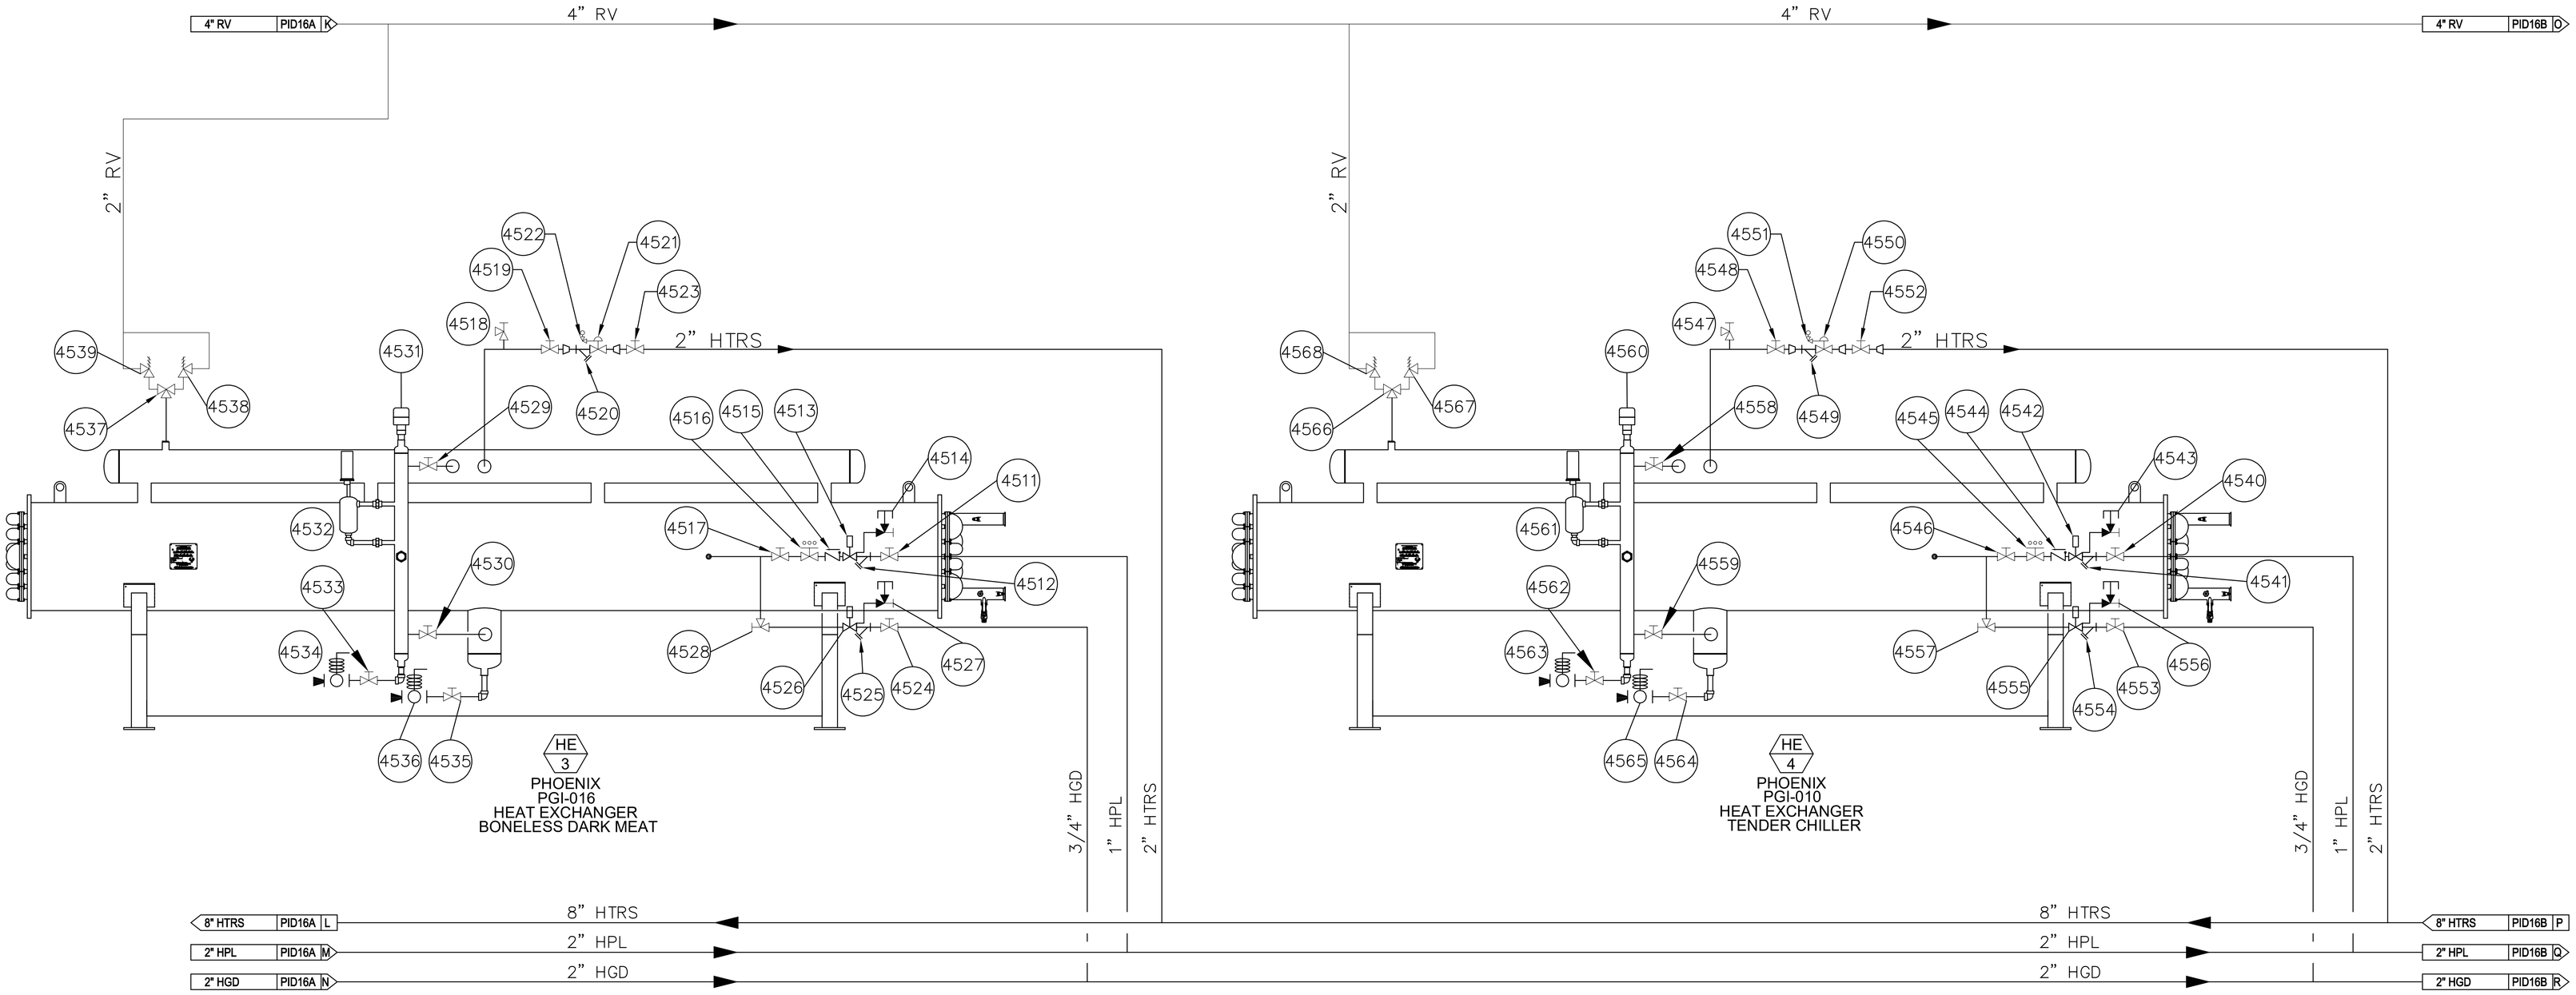


REVISIONS

NO.	DATE	DESCRIPTION	BY
1	9/20/25	ADD HE-1 TO HE-5	JIM

SCALE: NONE
DESIGNED BY: JIM S
DRAWN BY: JIM S
CHECKED BY: JIM S

Republic Refrigeration, Inc.
2810 Gray Fox Road Monroe, NC 28110
[704] 282-0399

WAYNE SANDERSON FARMS
UNION SPRINGS, AL

DRAWING DESCRIPTION
P&ID

DRAWING
PID16B

DATE
9/20/25

PROJECT NO.
CR2504H