


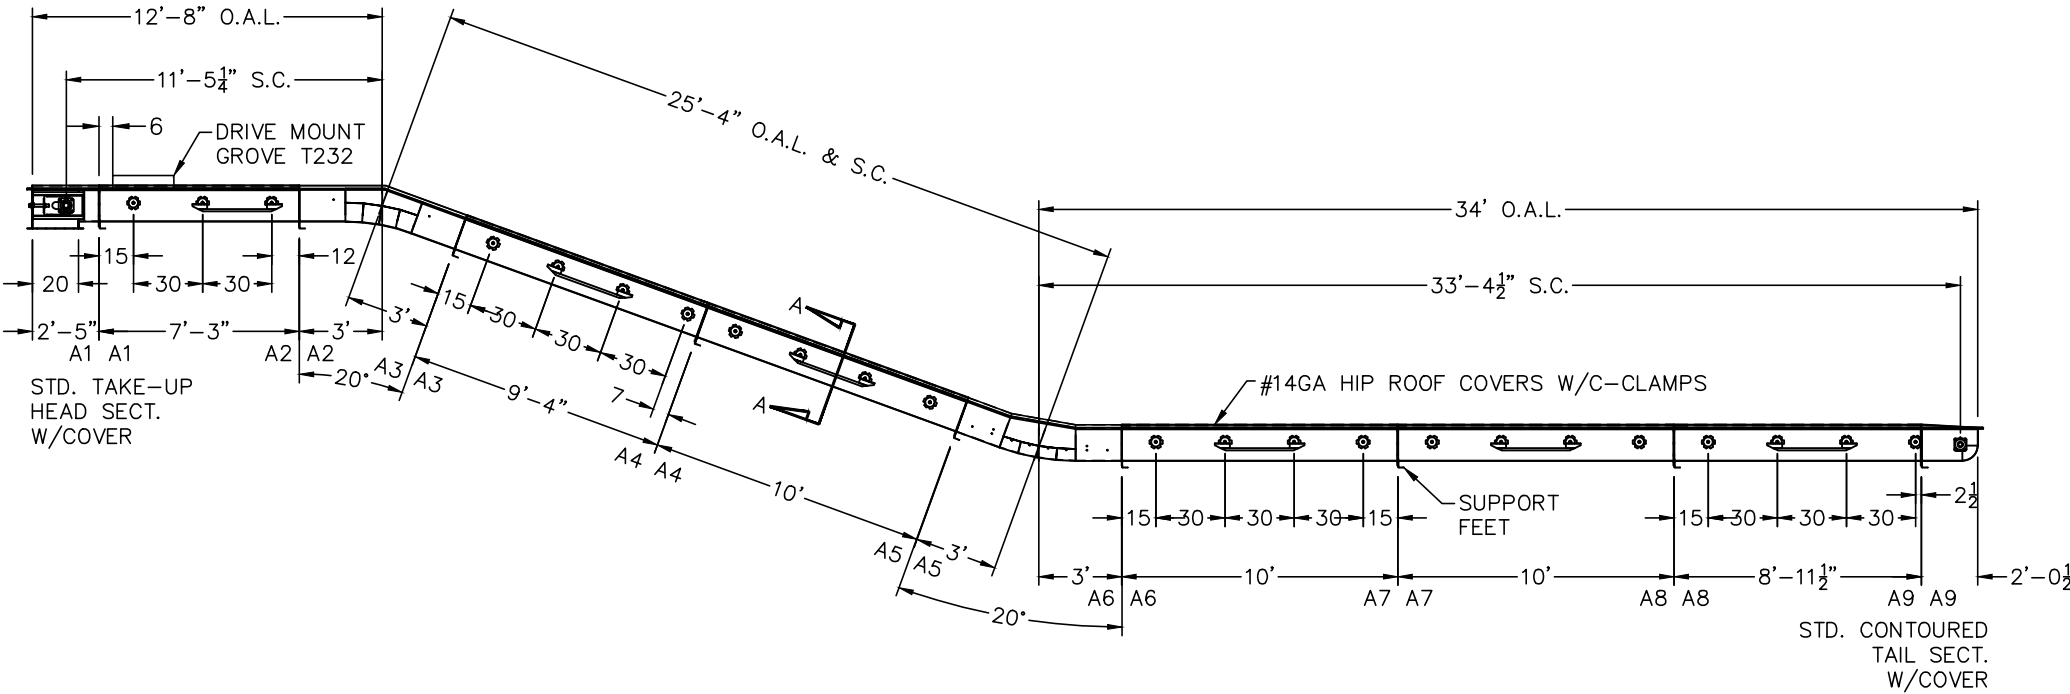

#10GA GALVANIZED MILD STEEL DOUBLE FLANGED TROUGH
SUPPORT FEET
#14GA HIP ROOF COVERS W/C-CLAMPS
CONTOURED TAIL SECT. W/RESTRICTOR PLATE
(1) 20° BEND SECTION
(1) 20° INVERTED BEND SECTION
INLET BY OTHERS
#10GA AR STEEL TROUGH LINER
DRIVE MOUNT FOR GROVE REDUCER
GALVANIZED CONSTRUCTION

NOTE: CONVEYORS ARE HOT DIPPED GALVANIZED-EXCEPT FOR COVERS, WHICH ARE MADE OF GALVANIZED STEEL.

CALCULATIONS BASED ON CHOKE LOAD (TOP OF FLITE CAPACITY)

INLET BY OTHERS #10GA AR STEEL TROUGH LINER DRIVE MOUNT FOR GROVE REDUCER GALVANIZED CONSTRUCTION		HP: 1.198		CAP: 500 CFH	DRN.BY: MP	THE ESSMUELLER COMPANY P.O.BOX 1966 LAUREL, MS. 39441 PH: (800)325-7175 FAX: (601)649-4320		
		RPM: 17		MAT: MATERIAL @ 60 PCF	DATE: 4/7/04			
		FPM: 34		INCLINE: 20°	REV:			
		(166) RB12" U.H.M.W. (HALF-SPACED)			(1) RB12" CONVEYOR X 70'-1 3/4" S.C.			
NOTE: CONVEYORS ARE HOT DIPPED GALVANIZED-EXCEPT FOR COVERS, WHICH ARE MADE OF GALVANIZED STEEL.		(14) STRANDS # C-188 COMBINATION CHAIN			(27) 12" STYLE 'A' IDLER ASSEMBLIES			
		(13) OF 48 W/12 ATT.,(1) OF 40 W/10 ATT.			(9) SUPPORTS (50) COVER CLAMPS			
		TOTAL CHAIN LENGTH: 144'-4 3/8"			DRIVE SUPPLIED BY: OTHERS			
CUSTOMER:	SHIP TO:	T-U HEAD W/ Ø2-3/16" R.H. FAR SIDE EXT.			CUST. P.O. NO: 38085		MK: A	
CAMPBELL SALES & SERVICE	WAYNE FARMS	6" EXT. FULLY KEYED			DRAWING NO: 04-0747		SHT: 1	
P.O. BOX 488	LOCK & SARDIS ROAD							
ATHENS, GA. 30601	UNION SPRINGS, AL 36089							